


PLOT PLAN

SCALE: 1/8" = 1'-0"

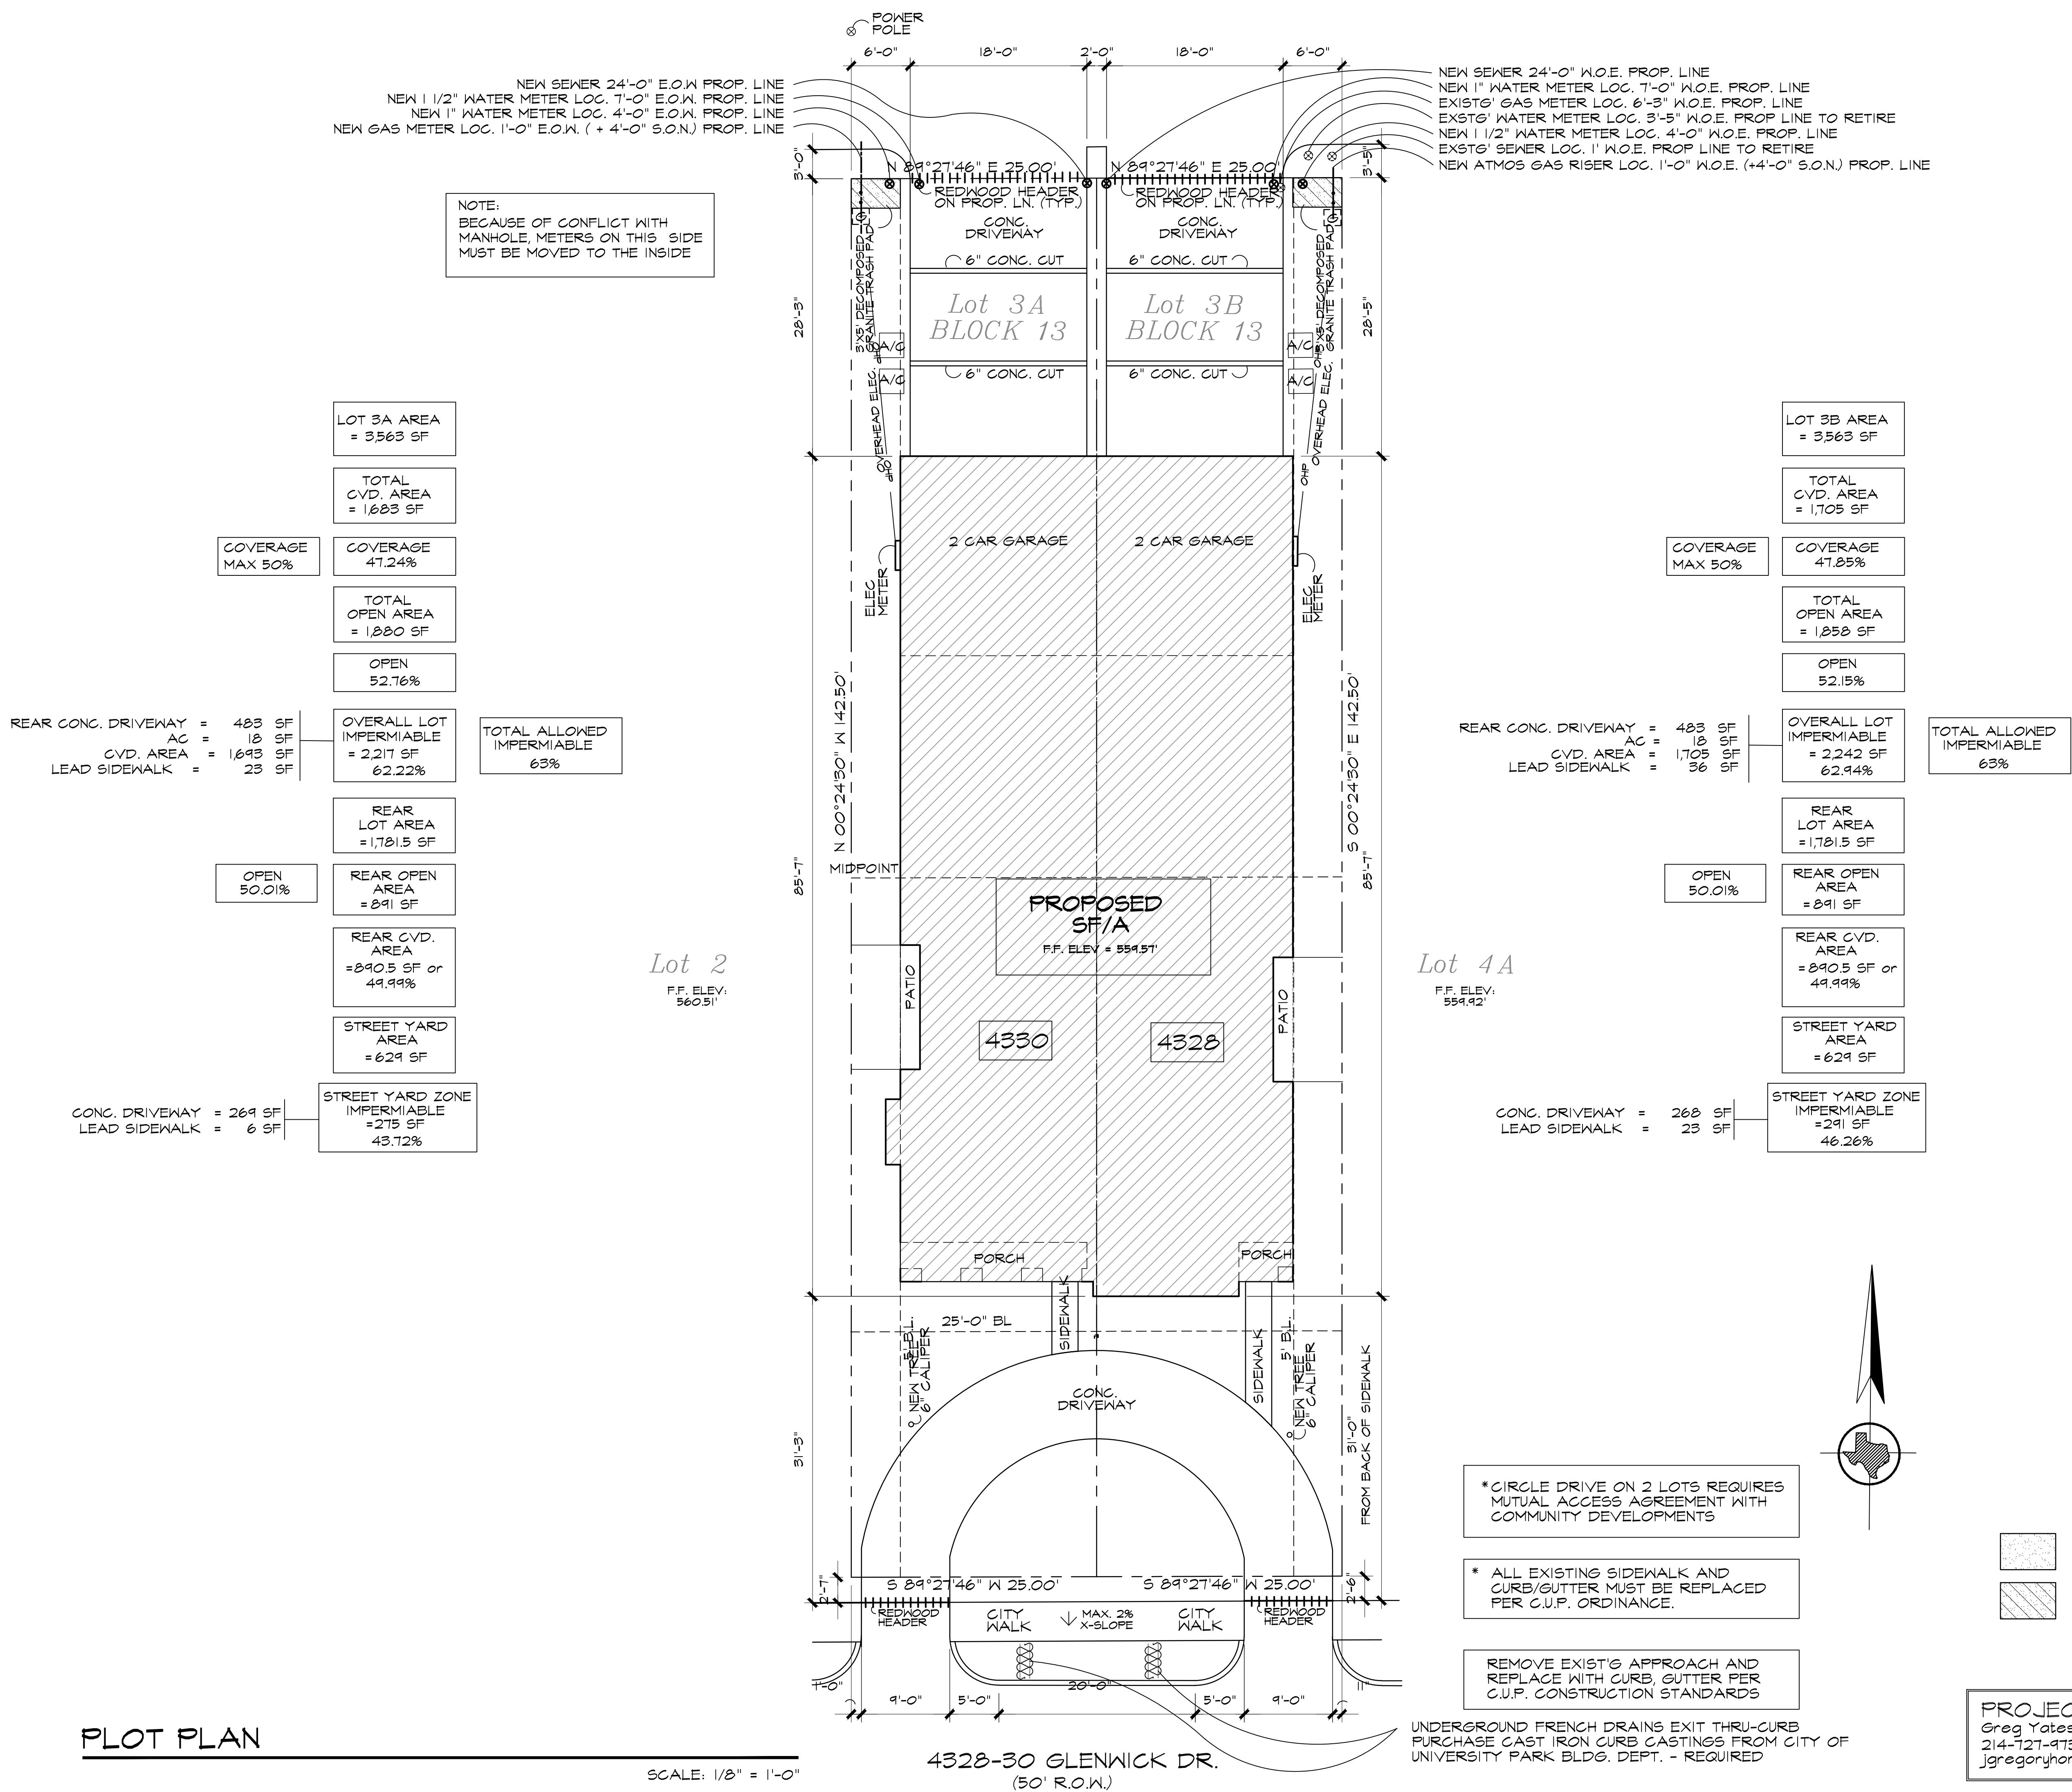

DATE 11/8/24
Red Line
NAME
REVISIONS
11/7/25
3/7/25
4/11/25


Glenwick Drive SF/A
JGH LLC/JG Residential Properties, LLC
4328-30 Glenwick Drive
Lot 3 Block 13 of Highland Park HS Add. Dallas, TX



IKEMIRE ARCHITECTS, PLLC
ARCHITECTURE
16660 DALLAS PKWY. SUITE 2900 DALLAS, TX 75248-2486
PLANNING
972-248-2486
INTERIORS
972-248-1557

WINDOW SCHEDULE

UNIT 432B	MARK	OPENING SIZE	HEADER HT. A.F.F.	TYPE	FLOOR	FRAME MATL.	FRAME FINISH	WINDOW TOTAL
	A	7'-6" x 7'-6"	8'-0"	FIXED - TEMPERED - ARCH TOP - DIVIDED LITE	1ST	VINYL	PAINT	1
	A'	5'-0" x 7'-6"	8'-0"	FIXED - TEMPERED - DIVIDED LITE	1ST	VINYL	PAINT	2
	B	3'-0" x 6'-0"	8'-0"	CASEMENT	1ST	VINYL	PAINT	1
	C	3'-0" x 7'-6"	8'-0"	FIXED, TEMPERED	1ST	VINYL	PAINT	1
	D	NOT USED	-	-	-	-	-	-
	E	2'-6" x 5'-0"	7'-0"	CASEMENT, DIVIDED LITE	2ND	VINYL	PAINT	2
	E'	NOT USED	-	-	-	-	-	-
	F	3'-0" x 5'-0"	7'-0"	FIXED	2ND	VINYL	PAINT	1
	F'	3'-0" x 5'-0"	7'-0"	CASEMENT	2ND	VINYL	PAINT	4
	G	NOT USED	-	-	-	-	-	-
	H	2'-6" x 5'-0"	7'-0"	FIXED	2ND	VINYL	PAINT	1
	I	NOT USED	-	-	-	-	-	-
	J	2'-0" x 2'-0"	7'-0"	FIXED	2ND	VINYL	PAINT	4
	J'	2'-0" x 3'-0"	7'-0"	FIXED	2ND	VINYL	PAINT	1
	K	3'-0" x 1'-0"	7'-0"	FIXED	2ND	VINYL	PAINT	2
	L	3'-0" x 5'-0"	7'-0"	CASEMENT	3RD	VINYL	PAINT	1
UNIT 433D	MARK	OPENING SIZE	HEADER HT. A.F.F.	TYPE	FLOOR	FRAME MATL.	FRAME FINISH	WINDOW TOTAL
	A	3'-6" x 7'-6"	8'-0"	FIXED - TEMPERED - ARCH TOP - DIVIDED LITE	1ST	VINYL	PAINT	2
	A'	3'-0" x 7'-6"	8'-0"	FIXED - TEMPERED - DIVIDED LITE	1ST	VINYL	PAINT	2
	B	3'-0" x 6'-0"	8'-0"	CASEMENT	1ST	VINYL	PAINT	1
	C	2'-6" x 7'-6"	8'-0"	FIXED, TEMPERED	1ST	VINYL	PAINT	1
	D	NOT USED	-	-	-	-	-	-
	E	2'-6" x 5'-0"	7'-0"	CASEMENT, DIVIDED LITE	2ND	VINYL	PAINT	2
	E'	2'-6" x 5'-0"	7'-0"	FIXED, DIVIDED LITE	2ND	VINYL	PAINT	1
	F	3'-0" x 5'-0"	7'-0"	CASEMENT	2ND	VINYL	PAINT	3
	F'	3'-0" x 5'-0"	7'-0"	FIXED	2ND	VINYL	PAINT	4
	G	2'-6" x 5'-0"	7'-0"	CASEMENT, DIVIDED LITE	2ND	VINYL	PAINT	2
	H	2'-6" x 5'-0"	7'-0"	FIXED	2ND	VINYL	PAINT	1
	I	NOT USED	-	-	-	-	-	-
	J	2'-0" x 2'-0"	7'-0"	FIXED	2ND	VINYL	PAINT	4
	J'	2'-0" x 3'-0"	7'-0"	FIXED	2ND	VINYL	PAINT	1
	K	3'-0" x 1'-0"	7'-0"	FIXED	2ND	VINYL	PAINT	2
	L	3'-0" x 5'-0"	7'-0"	CASEMENT	3RD	VINYL	PAINT	2

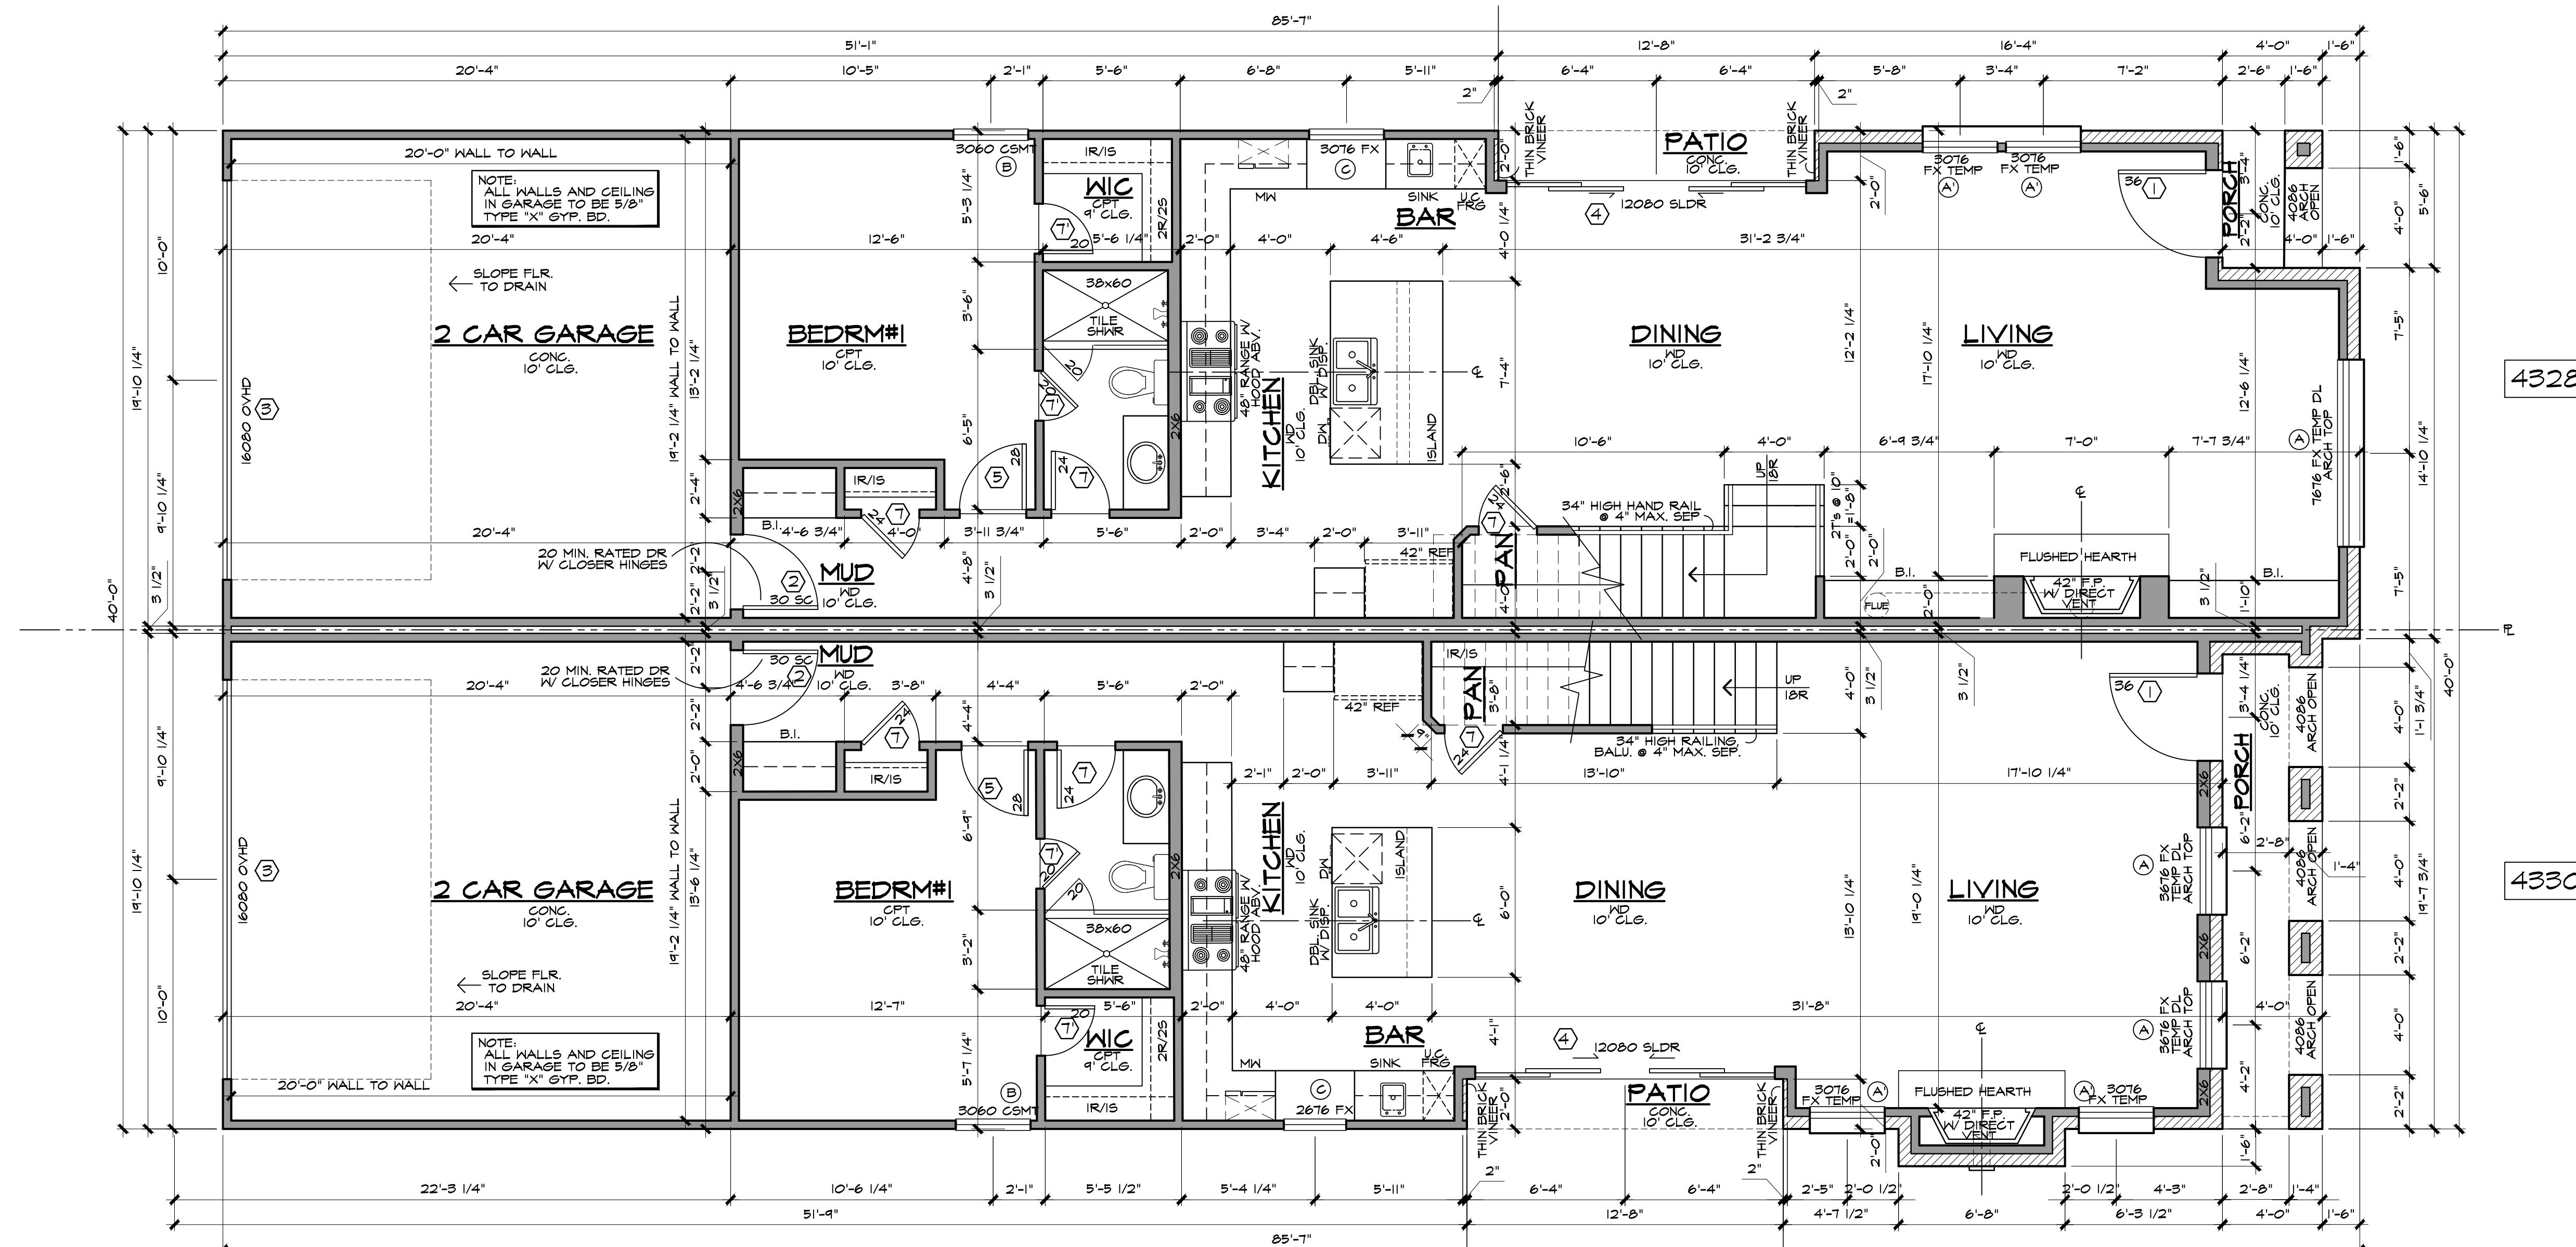

FIRST FLOOR PLAN

SCALE: 1/4" = 1'-0"

UNIT 432B	
FIRST FLOOR A/C	1,250 S.F.
SECOND FLOOR A/C	1,703 S.F.
THIRD FLOOR A/C	482 S.F.
TOTAL HOUSE A/C	3,435 S.F.
GARAGE	407 S.F.
CVD. PATIO	26 S.F.
PORCH	22 S.F.
TOTAL HOUSE S.F.	3,890 S.F.


UNIT 4330	
FIRST FLOOR A/C	1,174 S.F.
SECOND FLOOR A/C	1,683 S.F.
THIRD FLOOR A/C	482 S.F.
TOTAL HOUSE A/C	3,339 S.F.
GARAGE	407 S.F.
CVD. PATIO	26 S.F.
PORCH	76 S.F.
TOTAL HOUSE S.F.	3,848 S.F.

GENERAL 1ST FLR. PLAN NOTES:

1. TYP. STUD WALLS ARE 2x4'S, DIMENSIONED 4". EXTERIOR WALLS ARE 2x6'S, DIMENTIONED 6". OTHERS AS DIMENSIONED. BRICK VENEER IS 6".
2. INSTALL ALL 1ST FLR. WINDOWS WITH HEADS AT 8'-0" A.F.F. U.N.O.
3. ALL DOORS ON 1ST FLR. TO BE 8'-0" TALL U.N.O.
4. TYP. 1ST F.F. EL. = 0'-0" U.N.O.
5. FLOOR SYSTEM ASSUMED TO BE 1'-2" U.N.O.



Glenwick Drive SF/A

JGH, LLC/JG Residential Properties, LLC
4328-30 Glenwick Drive

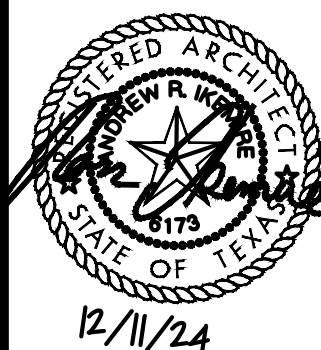

LIKEMIRE ARCHITECTS PLLC
 ARCHITECTURE ■ PLANNING ■ INTERIORS
 6660 DALLAS PKWY. SUITE 2900 DALLAS, TX 75248-2486 FAX 972-248-1557

A1

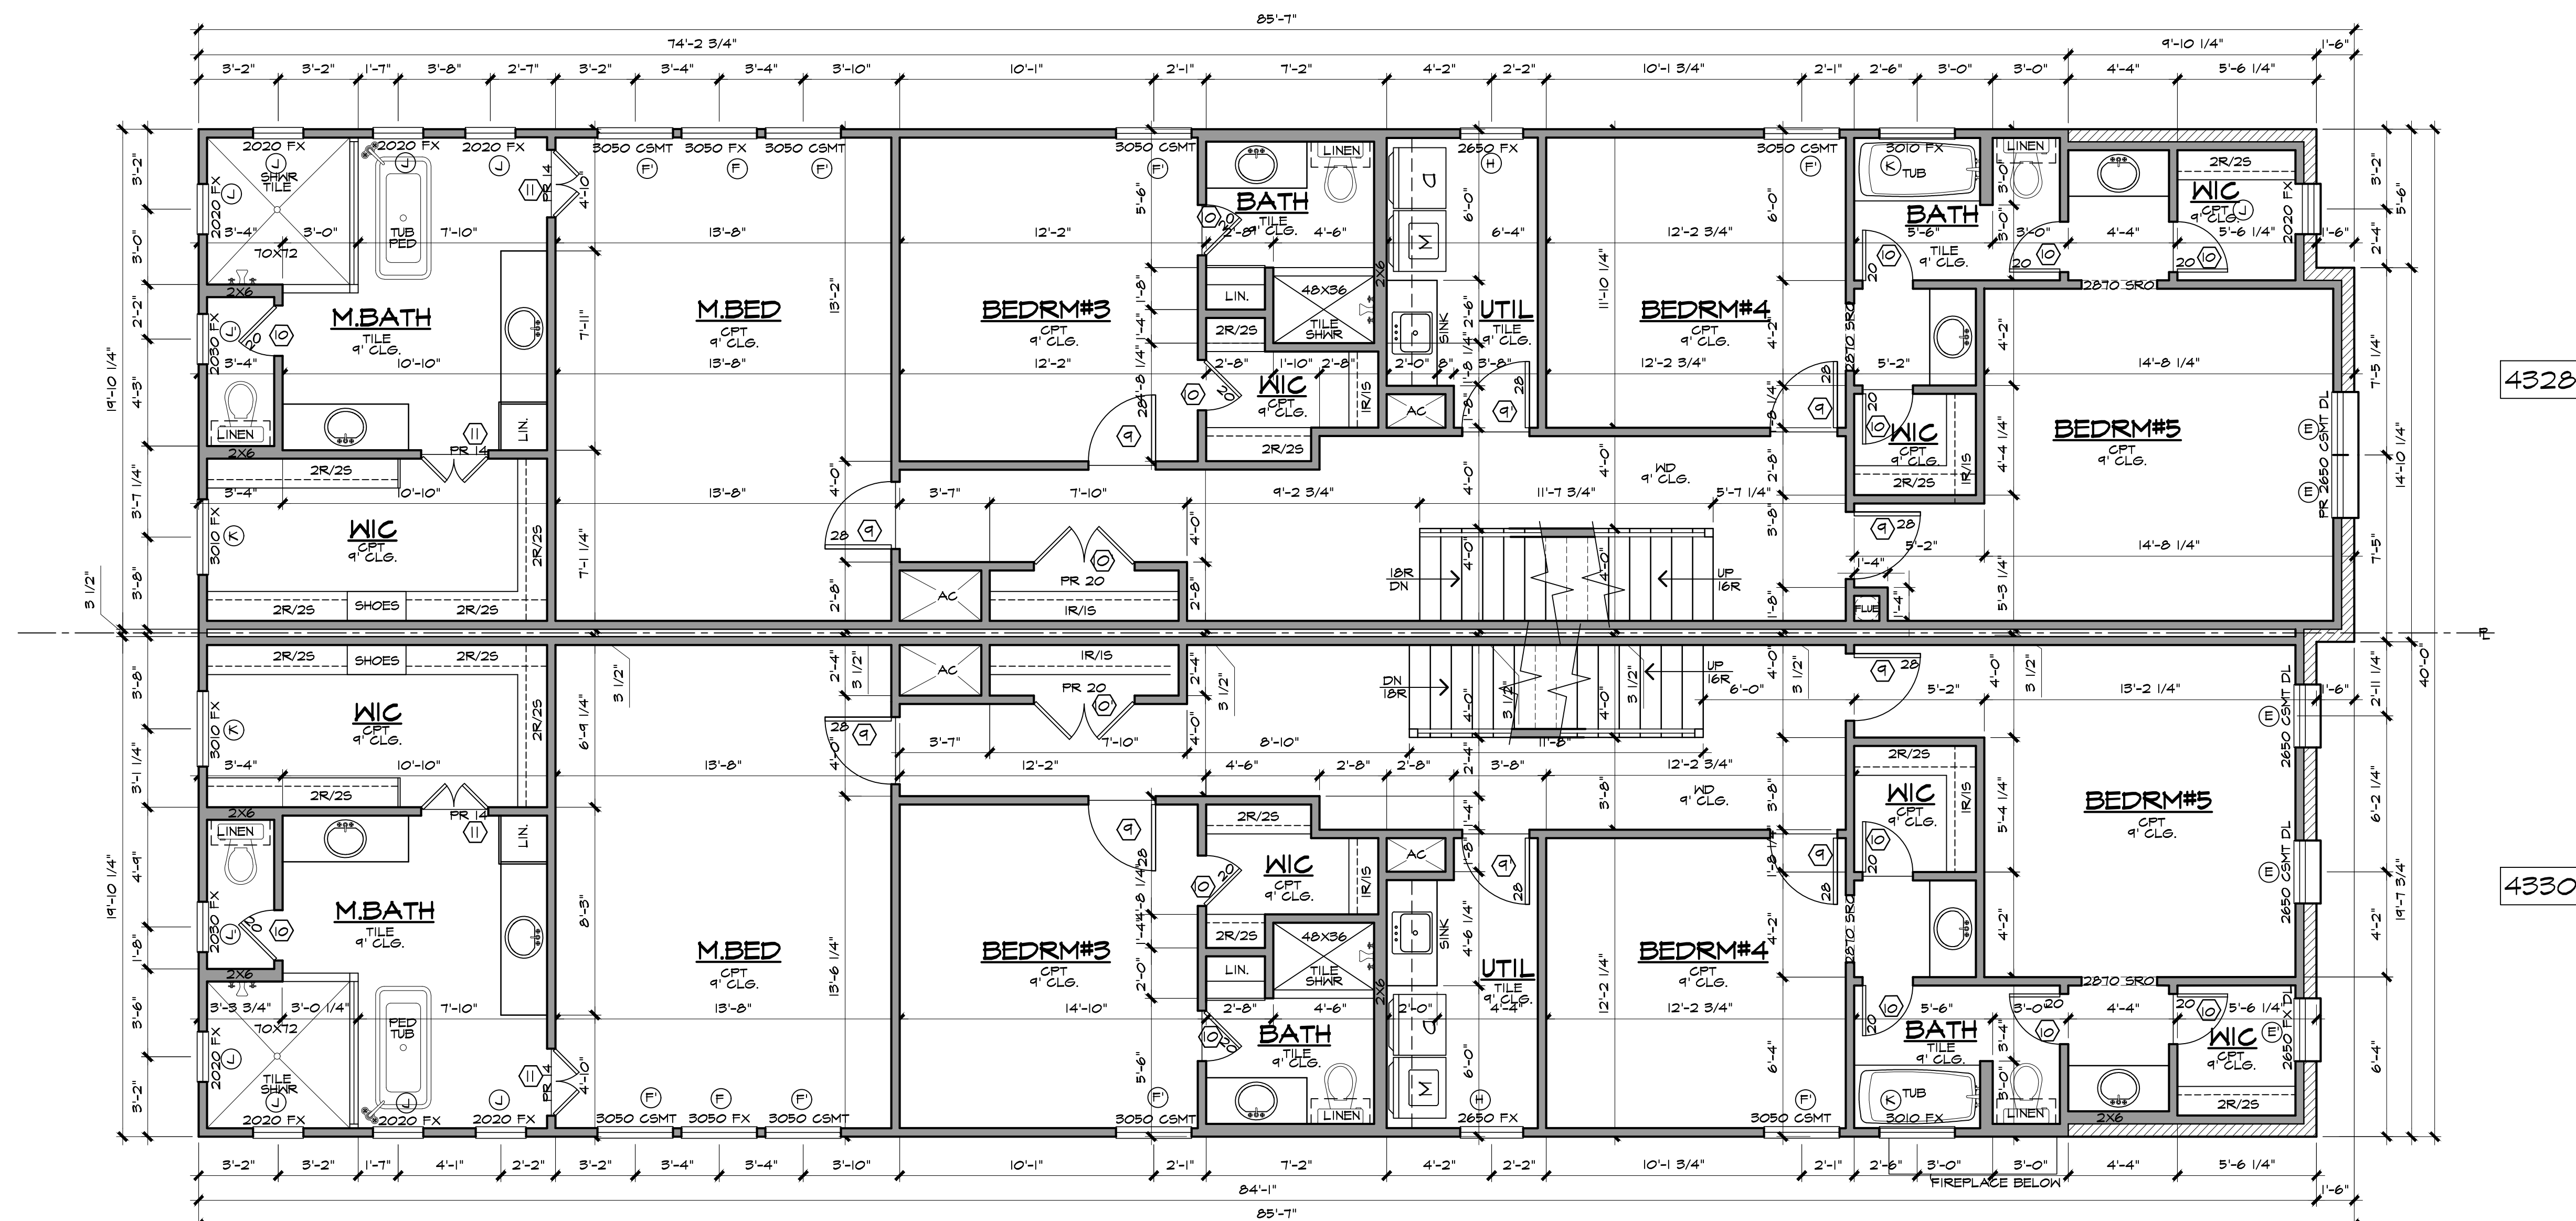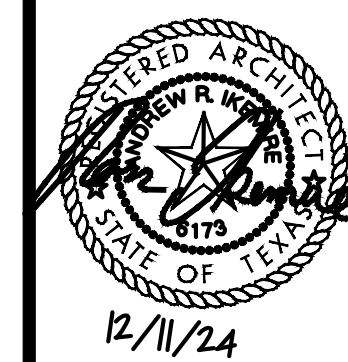


SECOND FLOOR PLAN

SCALE: 1/4" = 1'-0"

GENERAL 2ND. FLR. PLAN NOTES:

1. ALL STUD WALLS TO BE 2X4'S DIMENSIONED 4". OTHERS AS DIMENSIONED. BRICK 4/OR STONE VENEER IS 6".
2. INSTALL ALL 2ND FLR. WINDOWS WITH HEADS AT 7'-0" A.F.F. U.N.O.
3. ALL DOORS ON 2ND FLR. TO BE 7'-0" TALL U.N.O.
4. TYP. 2ND F.F. EL. = 11'-2" U.N.O.
5. FLOOR SYSTEM ASSUMED TO BE 1'-2" U.N.O.

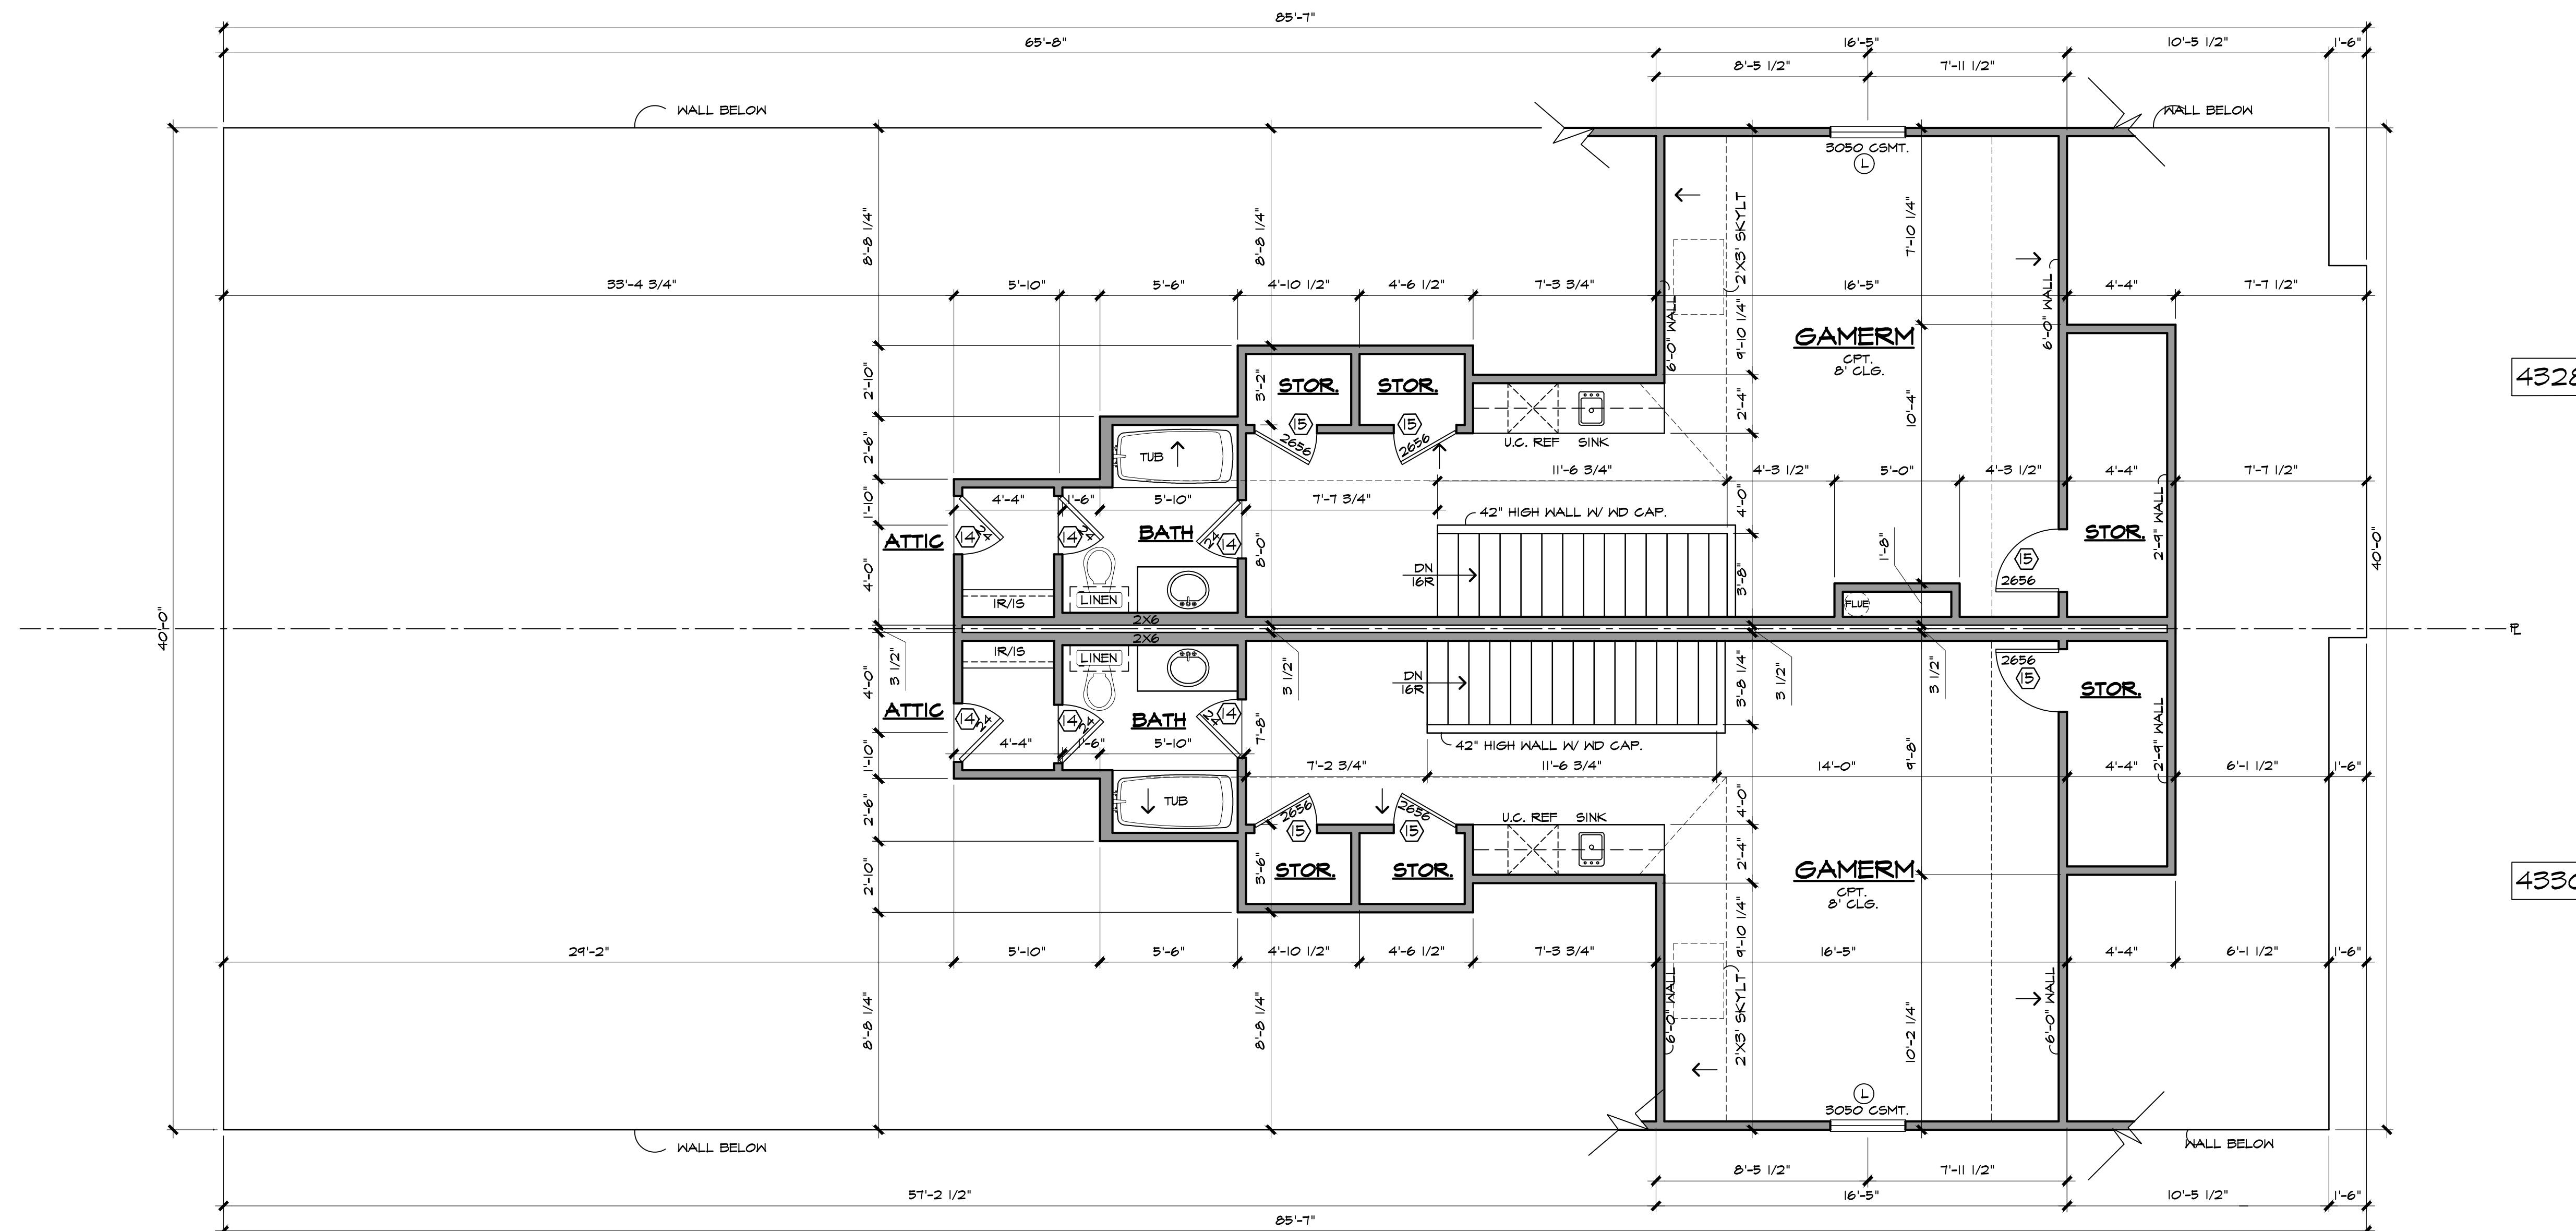

THIRD FLOOR PLAN

SCALE: 1/4" = 1'-0"

GENERAL 3RD FLR. PLAN NOTES:


1. ALL STUD WALLS TO BE 2X4'S DIMENSIONED 4". OTHERS AS DIMENSIONED. BRICK &/OR STONE VENEER IS 6".
2. INSTALL ALL 3RD FLR. WINDOWS WITH HEADS AT 6'-8" A.F.F. U.N.O.
3. ALL DOORS ON 3RD FLR. TO BE 6'-8" TALL U.N.O.
4. TYP. 3RD F.F. EL. = 22'-4" U.N.O.
5. FLOOR SYSTEM ASSUMED TO BE 1'-2" U.N.O.

DATE 11/8/24
Red Line
NAME
REVISIONS
1/17/25
5/7/25

Glenwick Drive SF/A
JGH, LLC/JG Residential Properties, LLC
4328-30 Glenwick Drive
Lot 5 Block 15 of Highland Park HS Add. Dallas, TX



IKEMIRE ARCHITECTS, LLC
ARCHITECTURE PLANNING INTERIORS
16660 DALLAS PKWY. SUITE 2900 DALLAS, TX 75248-2486 FAX 972-248-1557

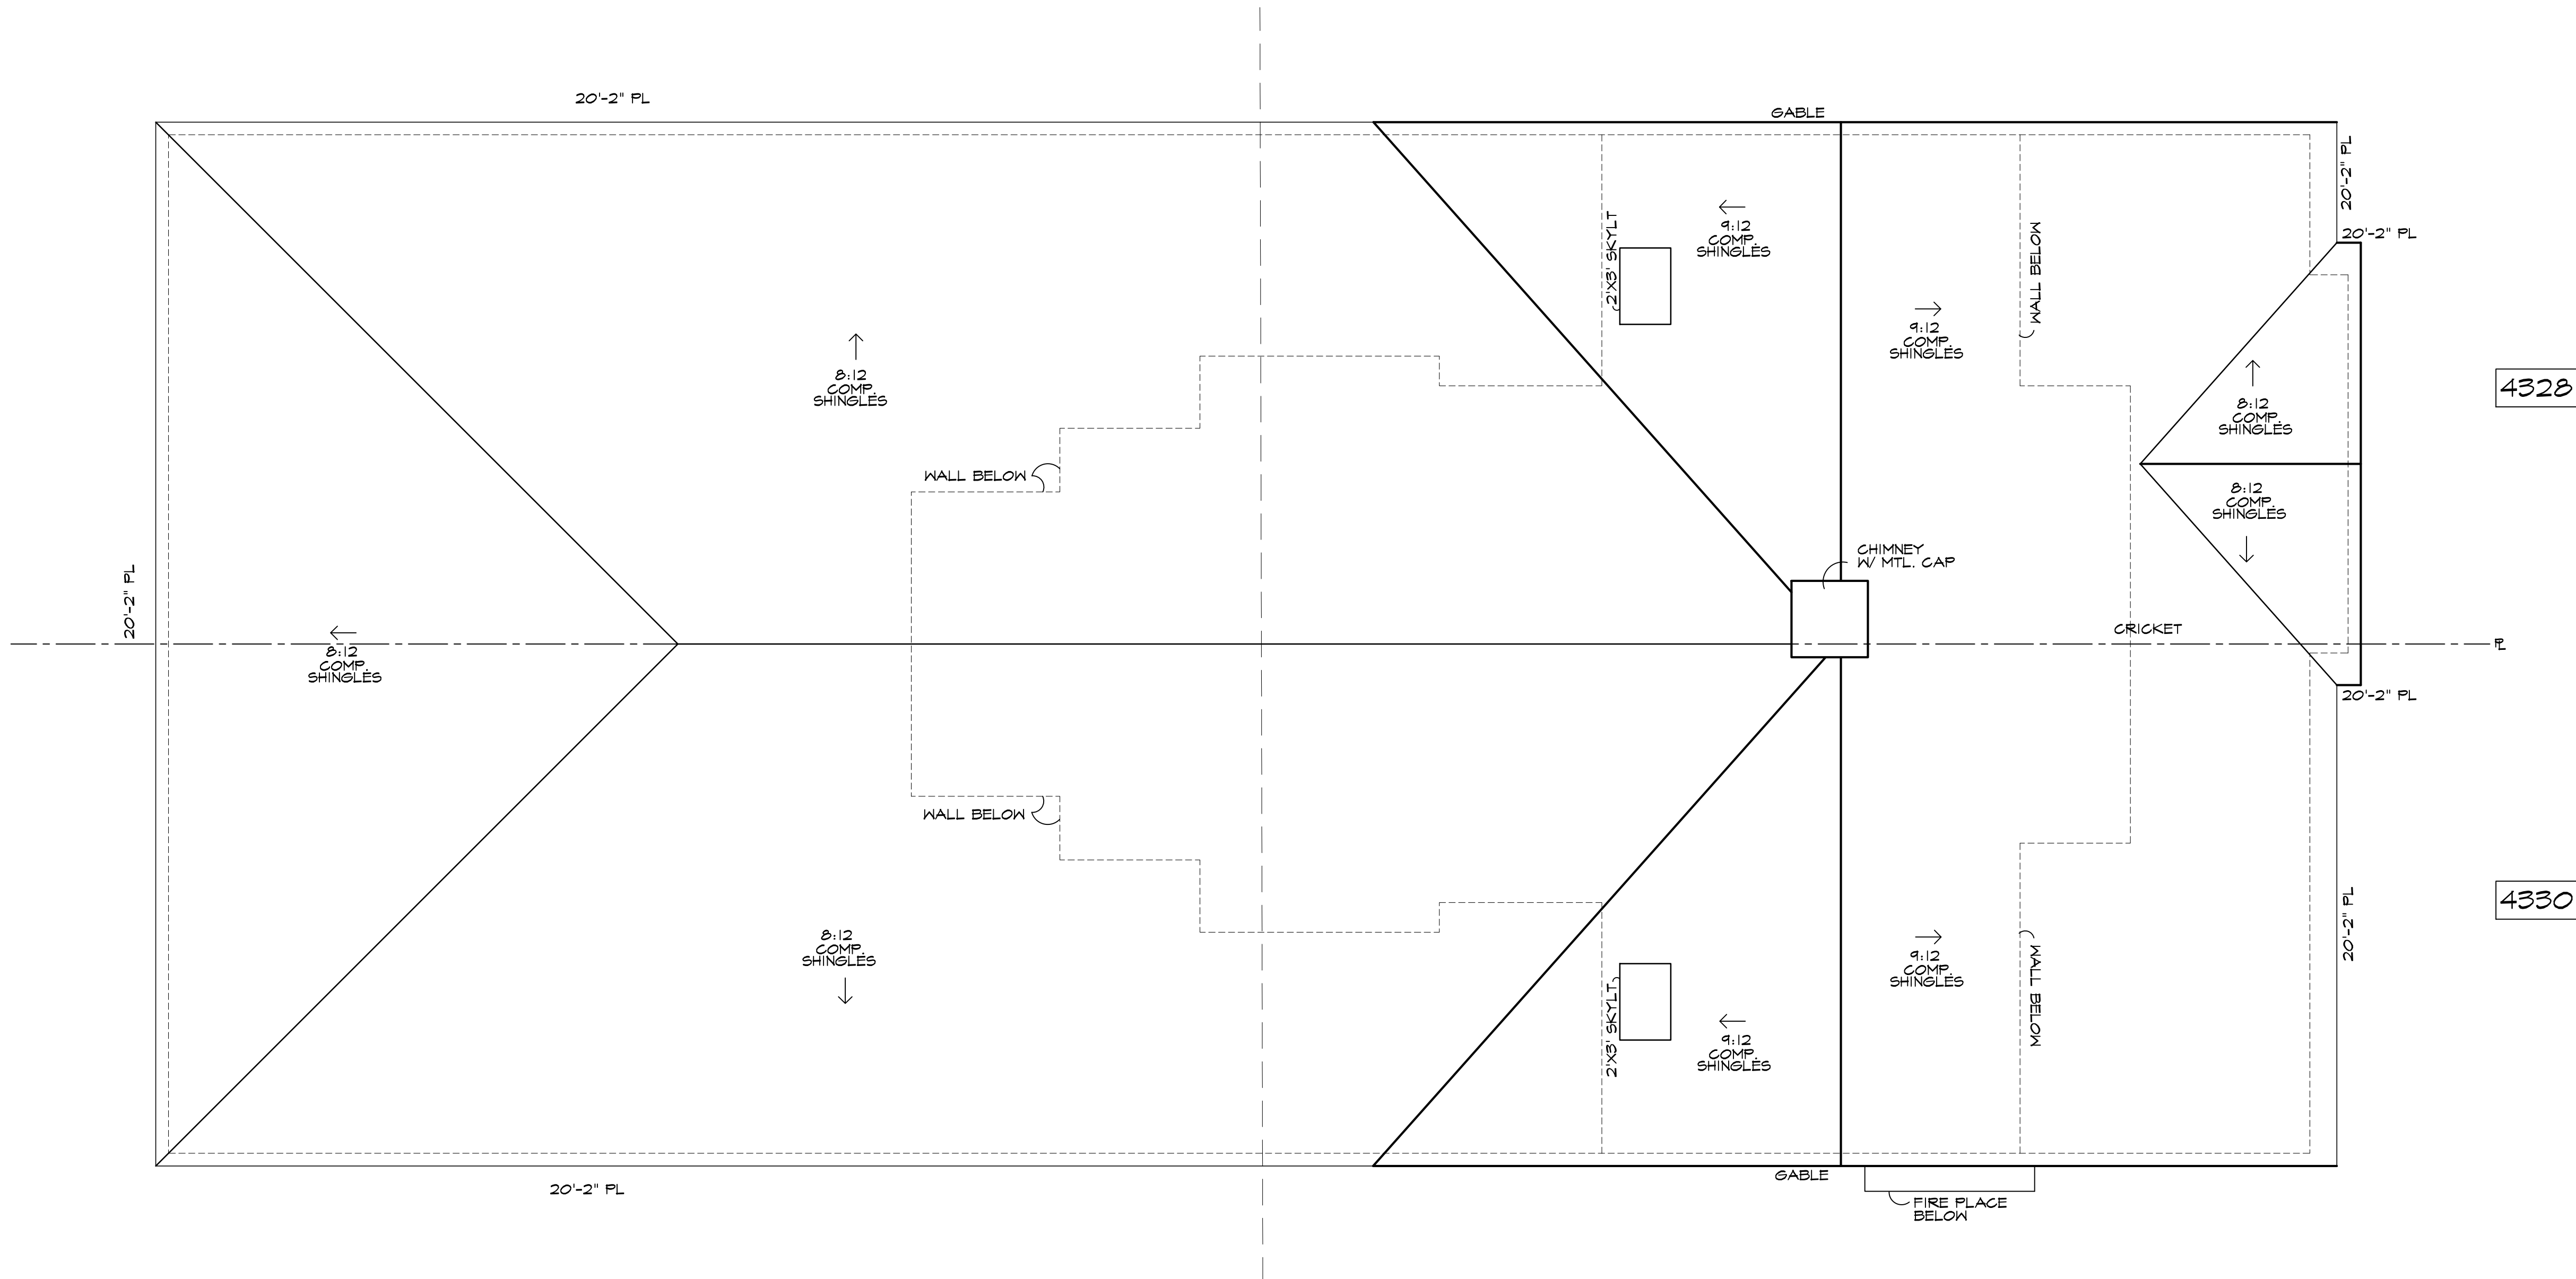

ROOF PLAN

1. ARROWS INDICATE ROOF SLOPE DOWNWARD
2. ALL ROOFING MATERIAL TO BE COMP. SHINGLES U.N.O.
3. BUILDER TO PROVIDE ENERGY STAR QUALIFIED ROOF MATERIALS.
4. HVAC UNIT TO BE LOCATED IN THE ATTIC SPACE.

SCALE: 1/4" = 1'-0"


DATE 11/8/24
Red Line
NAME
REVISIONS
11/17/25
5/17/25

Glenwick Drive SF/A
JGH, LLC/JG Residential Properties, LLC
4328-30 Glenwick Drive
Lot 5 Block 15 of Highland Park HS Add. Dallas, TX




IKEMIRE ARCHITECTS LLC
ARCHITECTURE PLANNING INTERIORS
16660 DALLAS PKWY. SUITE 2900 DALLAS, TX 75248-2486 FAX 972-248-1557

A4
5 of 13
JOB #224045

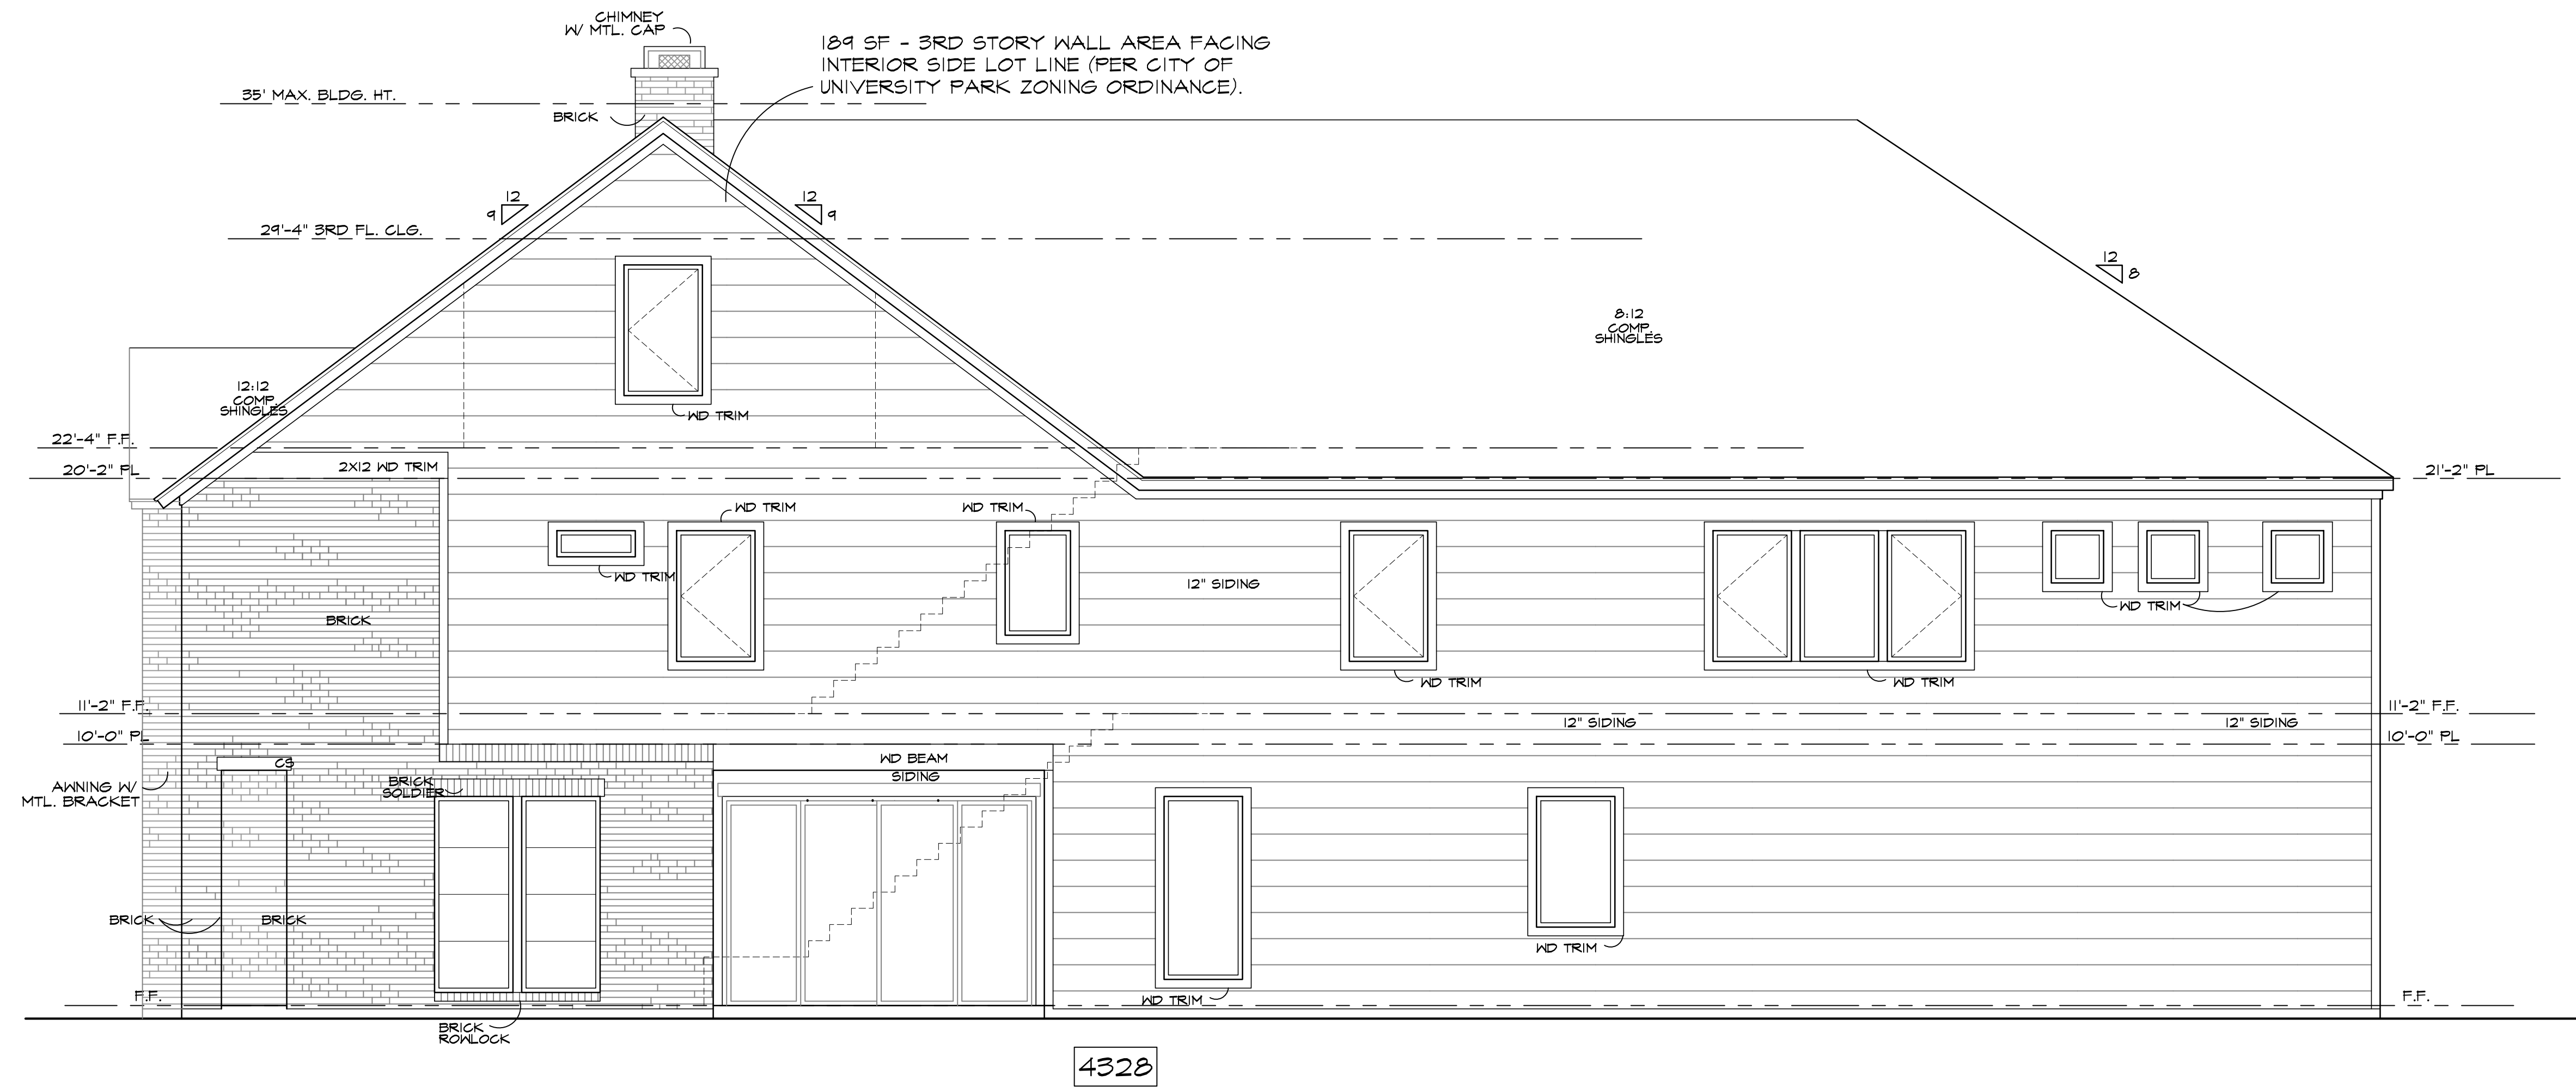

RIGHT ELEVATION

SCALE: 1/4" = 1'-0"

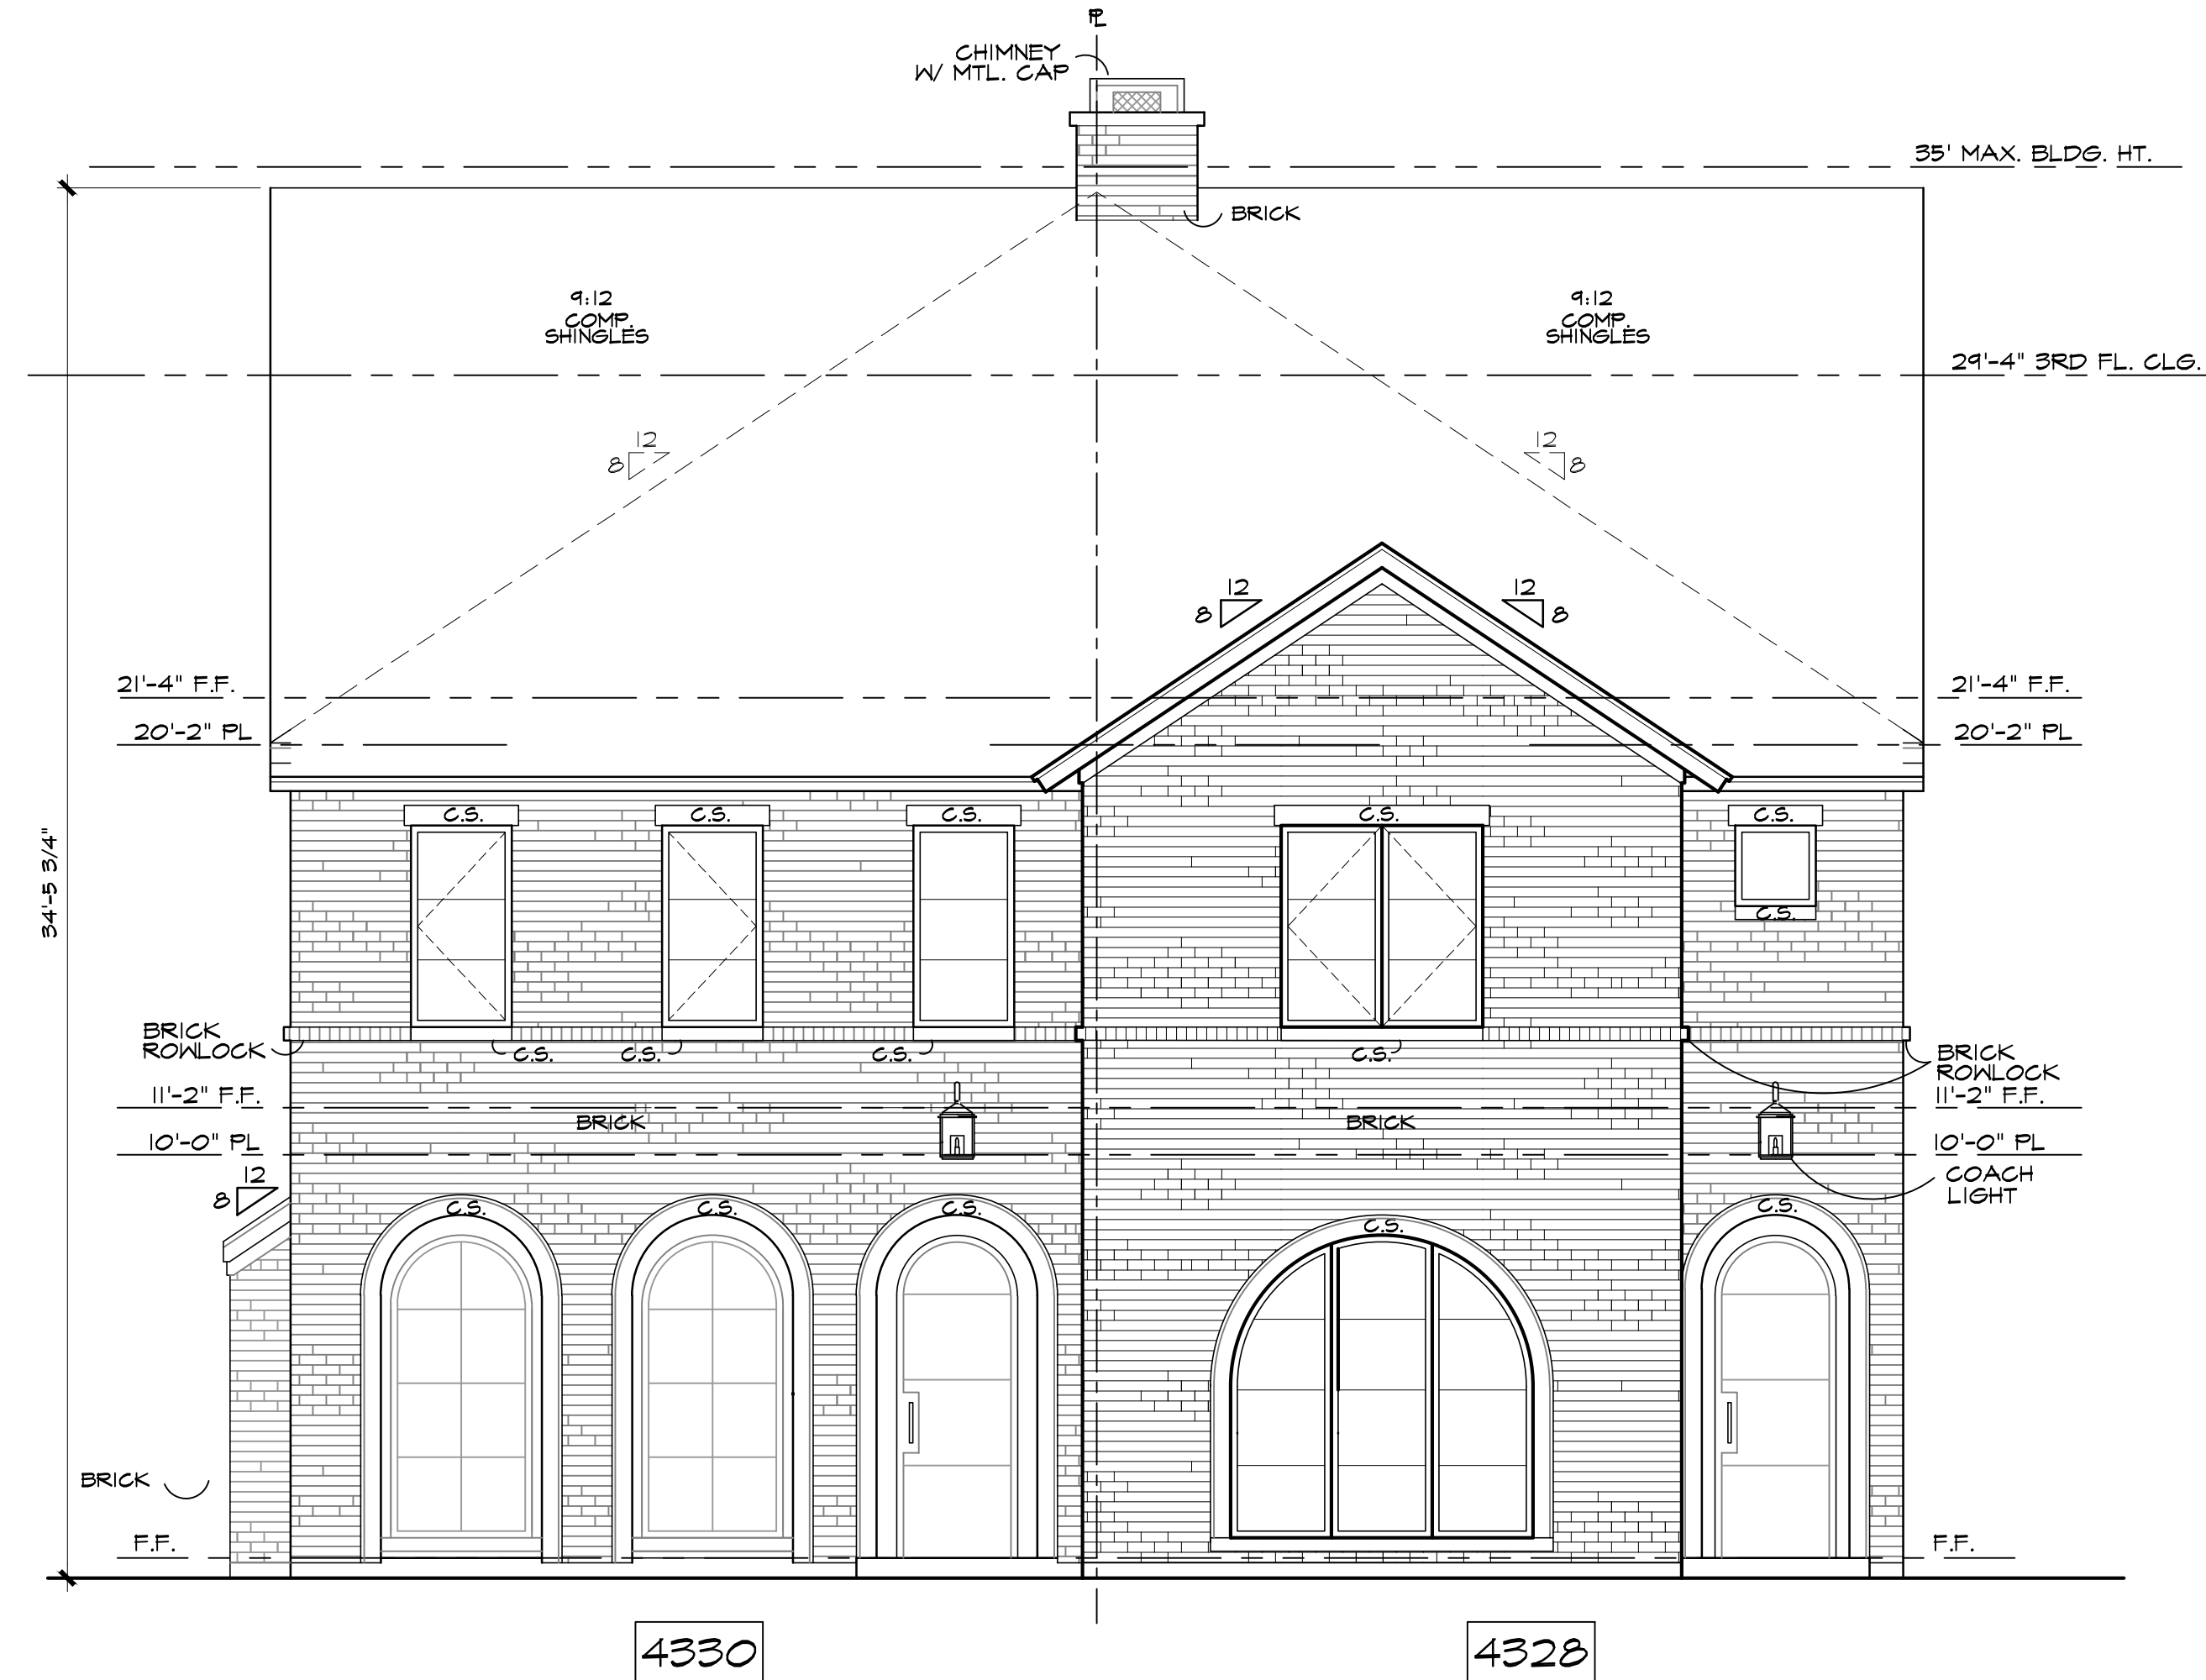

FRONT ELEVATION

SCALE: 1/4" = 1'-0"



DATE 11/8/24
Red Line
NAME
REVISIONS
11/17/25
5/1/25

Glenwick Drive SF/A
JGH, LLC/JG Residential Properties, LLC
4328-30 Glenwick Drive
Lot 5 Block 13 of Highland Park HS Add. Dallas, TX



IKEMIRE ARCHITECTS, LLC
ARCHITECTURE
16660 DALLAS PKWY. SUITE 2900 DALLAS, TX 75248-1557
PLANNING INTERIORS
972-248-2486 FAX 972-248-1557


A5
6 of 13
JOB #224045

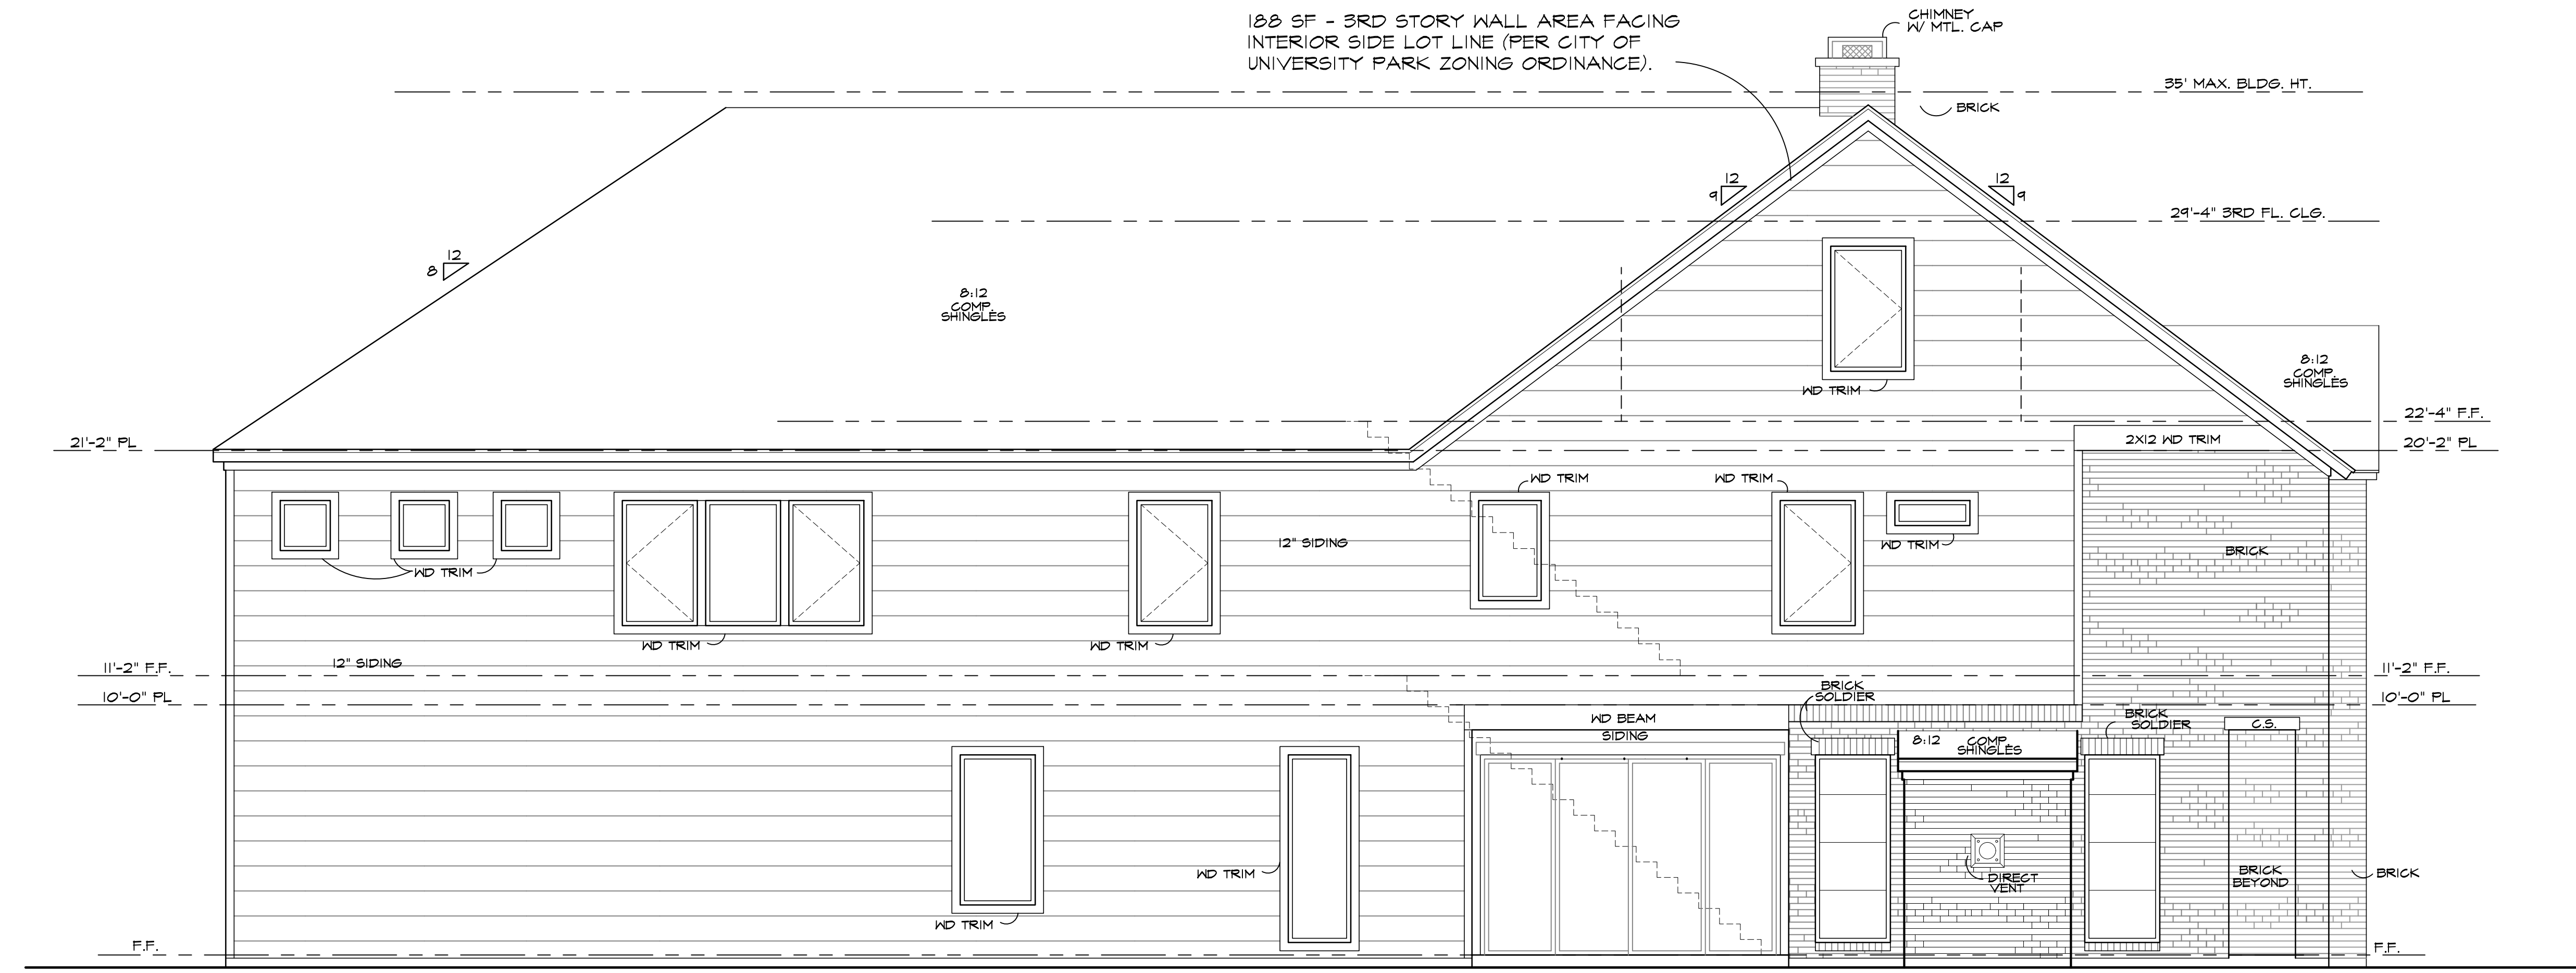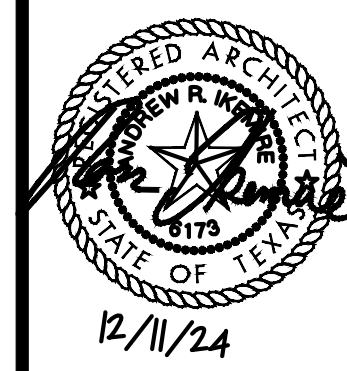

LEFT ELEVATION

SCALE: 1/4" = 1'-0"

4330

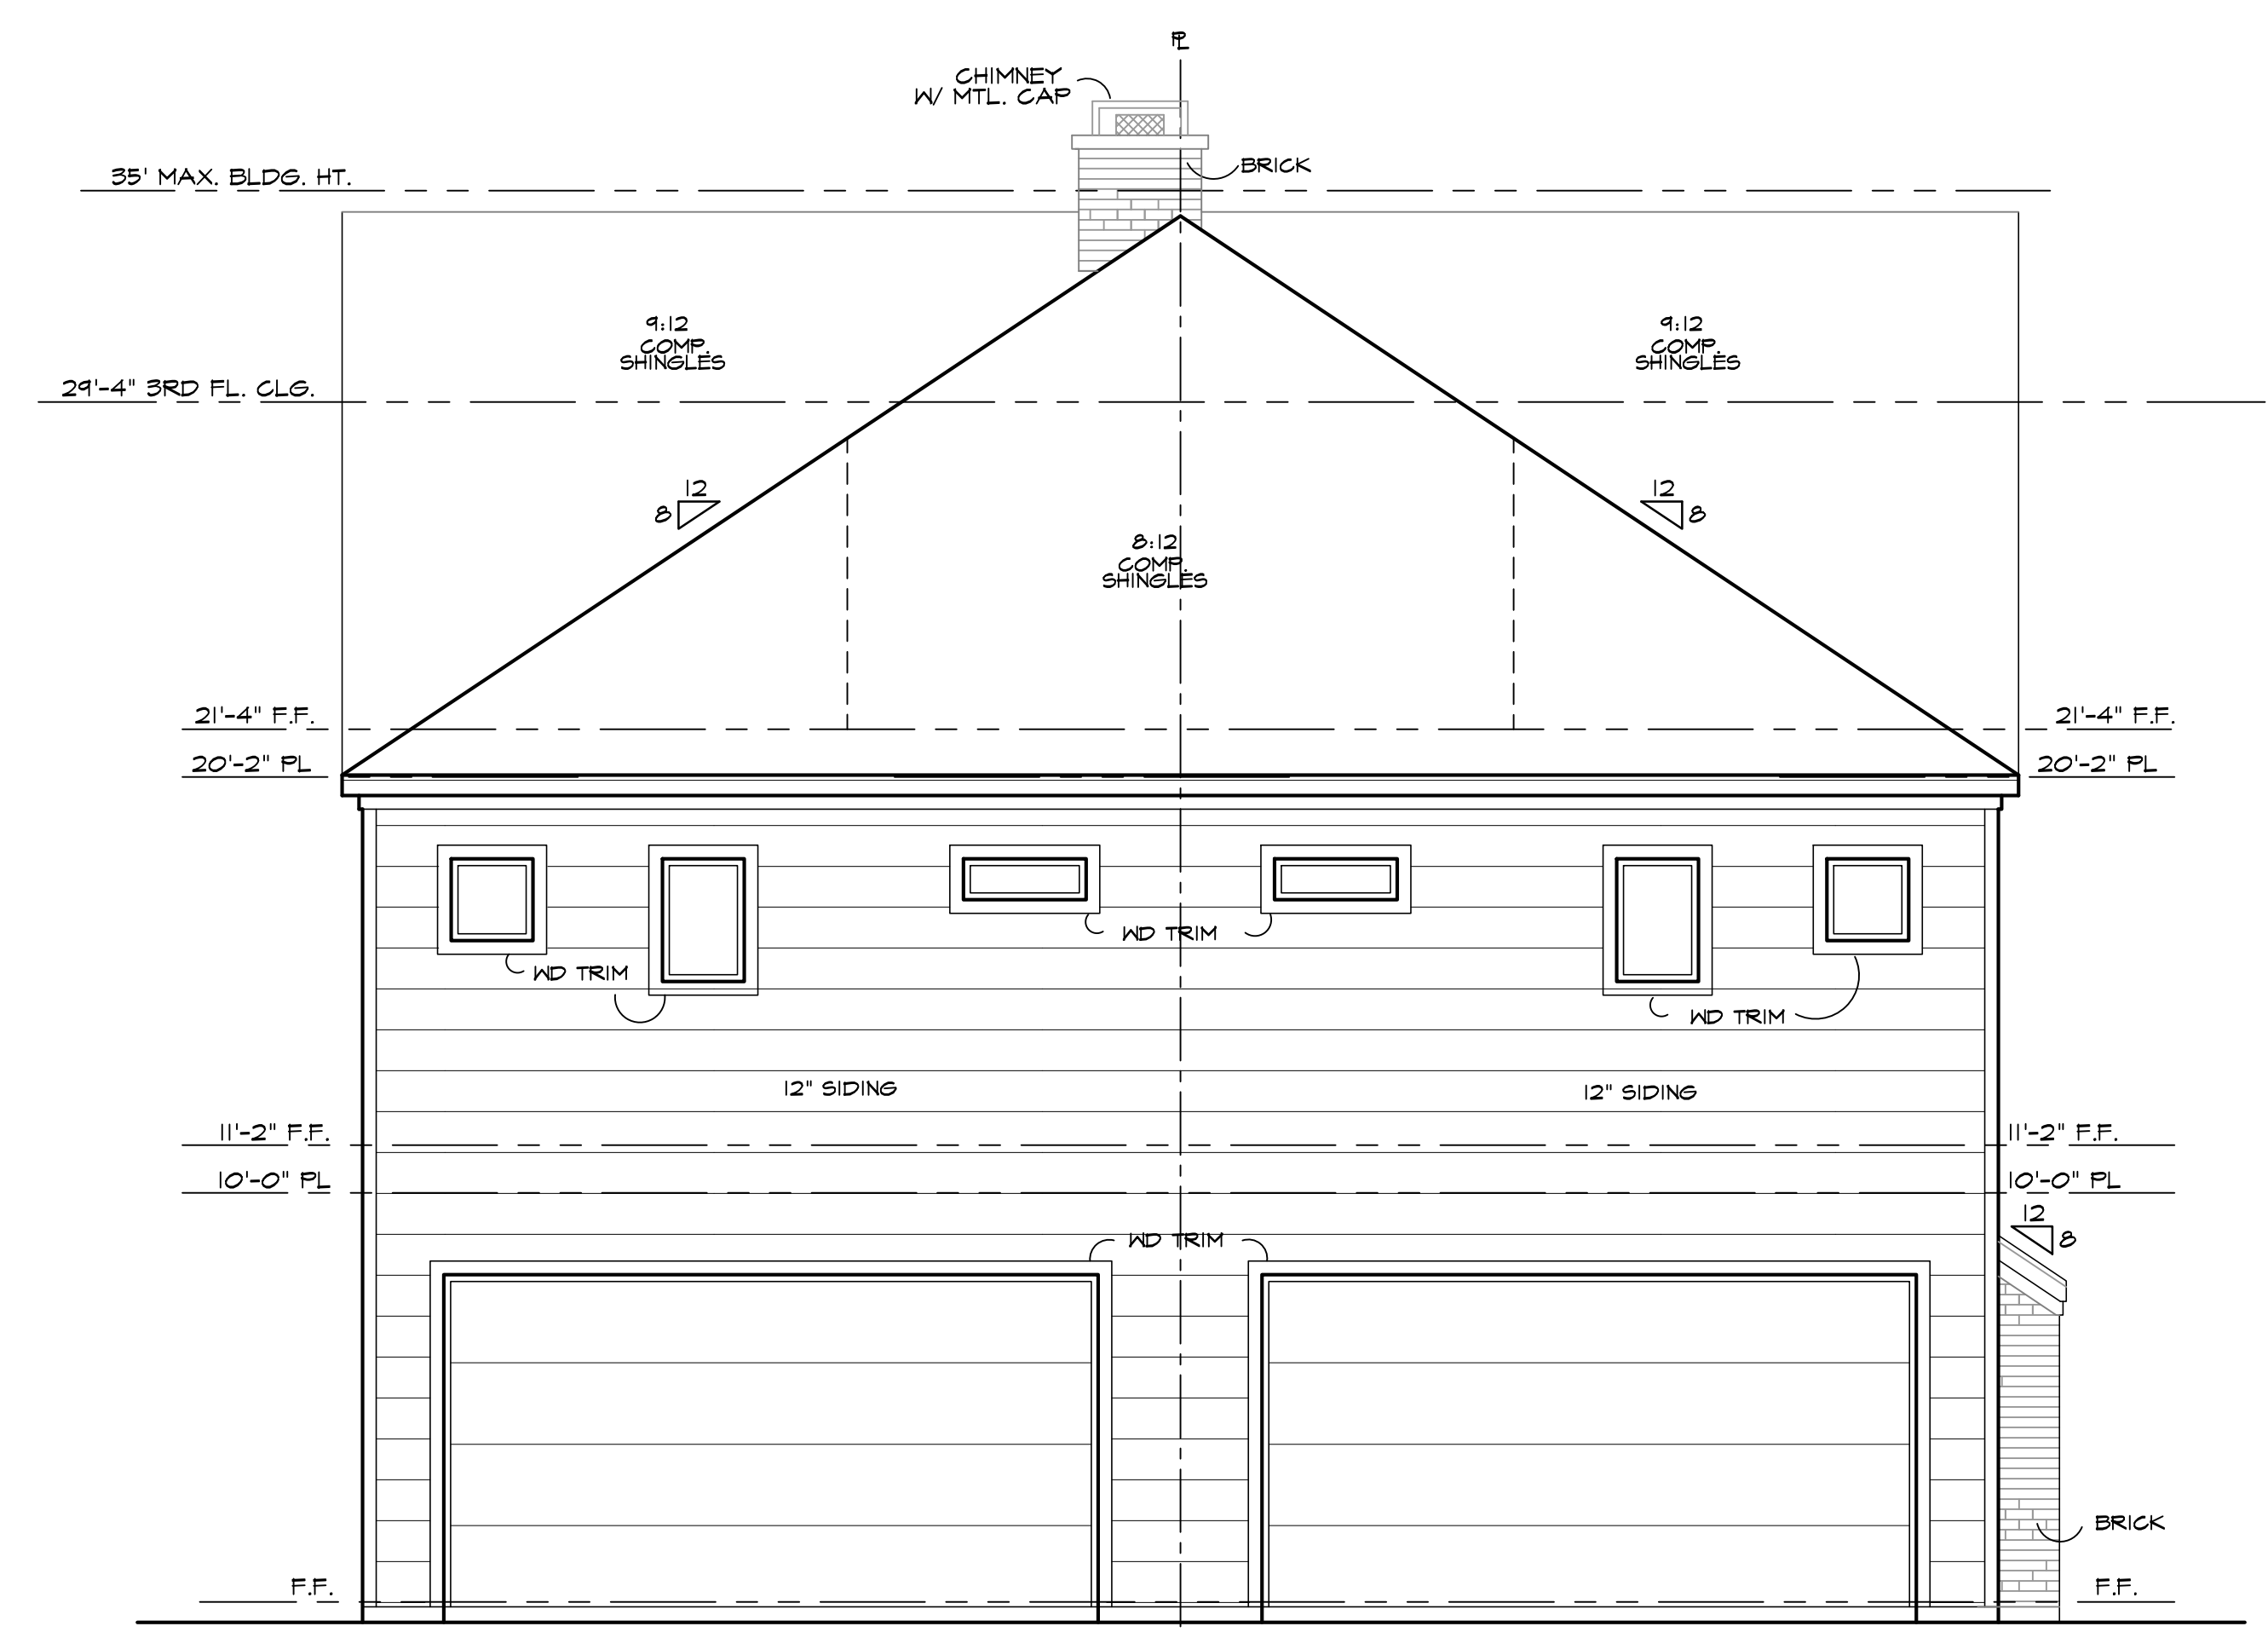


REAR ELEVATION


SCALE: 1/4" = 1'-0"

4328


4330

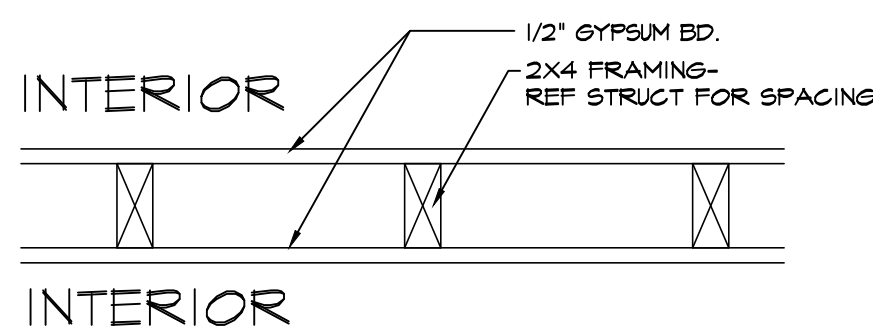


08 Typ. Interior Wall
SCALE: 1/2" = 1'-0"

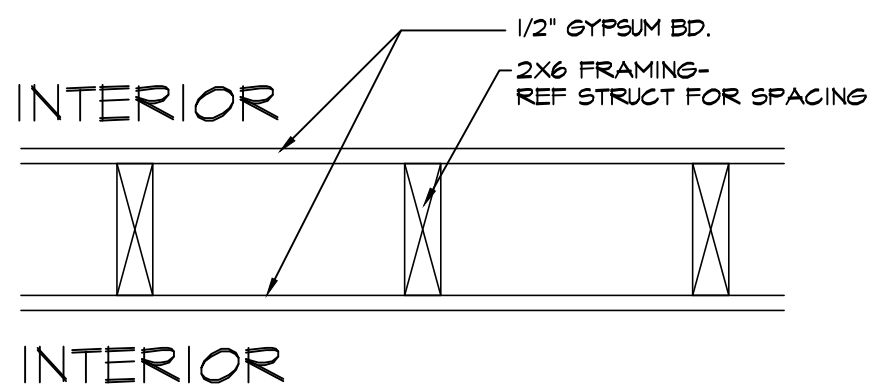


07 Typ. Interior Wall
SCALE: 1/2" = 1'-0"

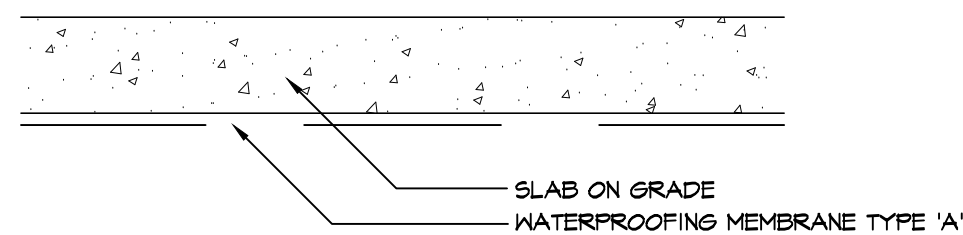


06 Typ. Foundation on Grade
SCALE: 1/2" = 1'-0"

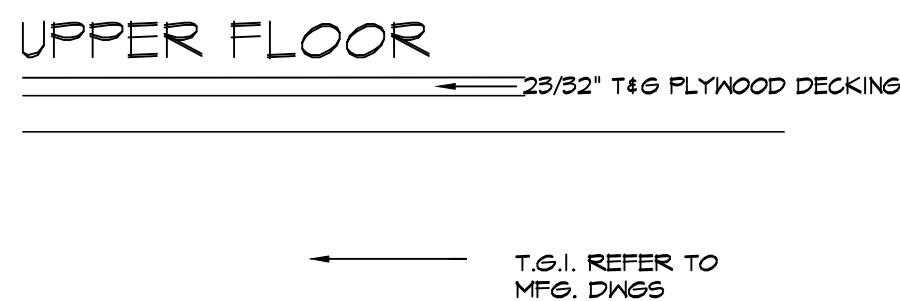


05 Typ. Mid Floor Without Insulation
SCALE: 1/2" = 1'-0"

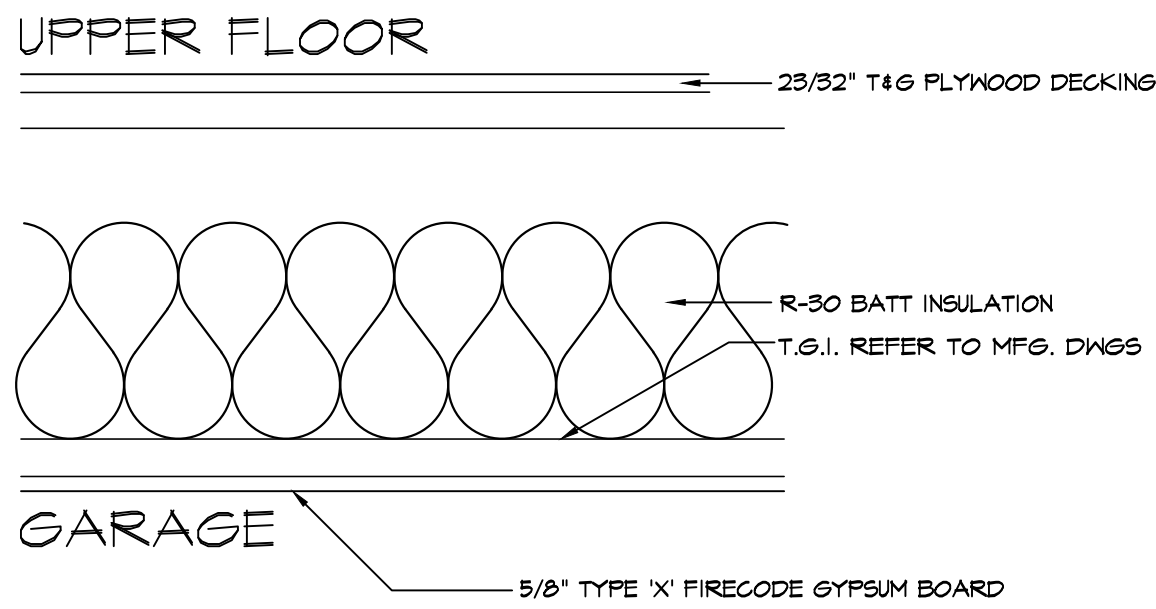

04 Typ. Mid Floor With Insulation
SCALE: 1/2" = 1'-0"

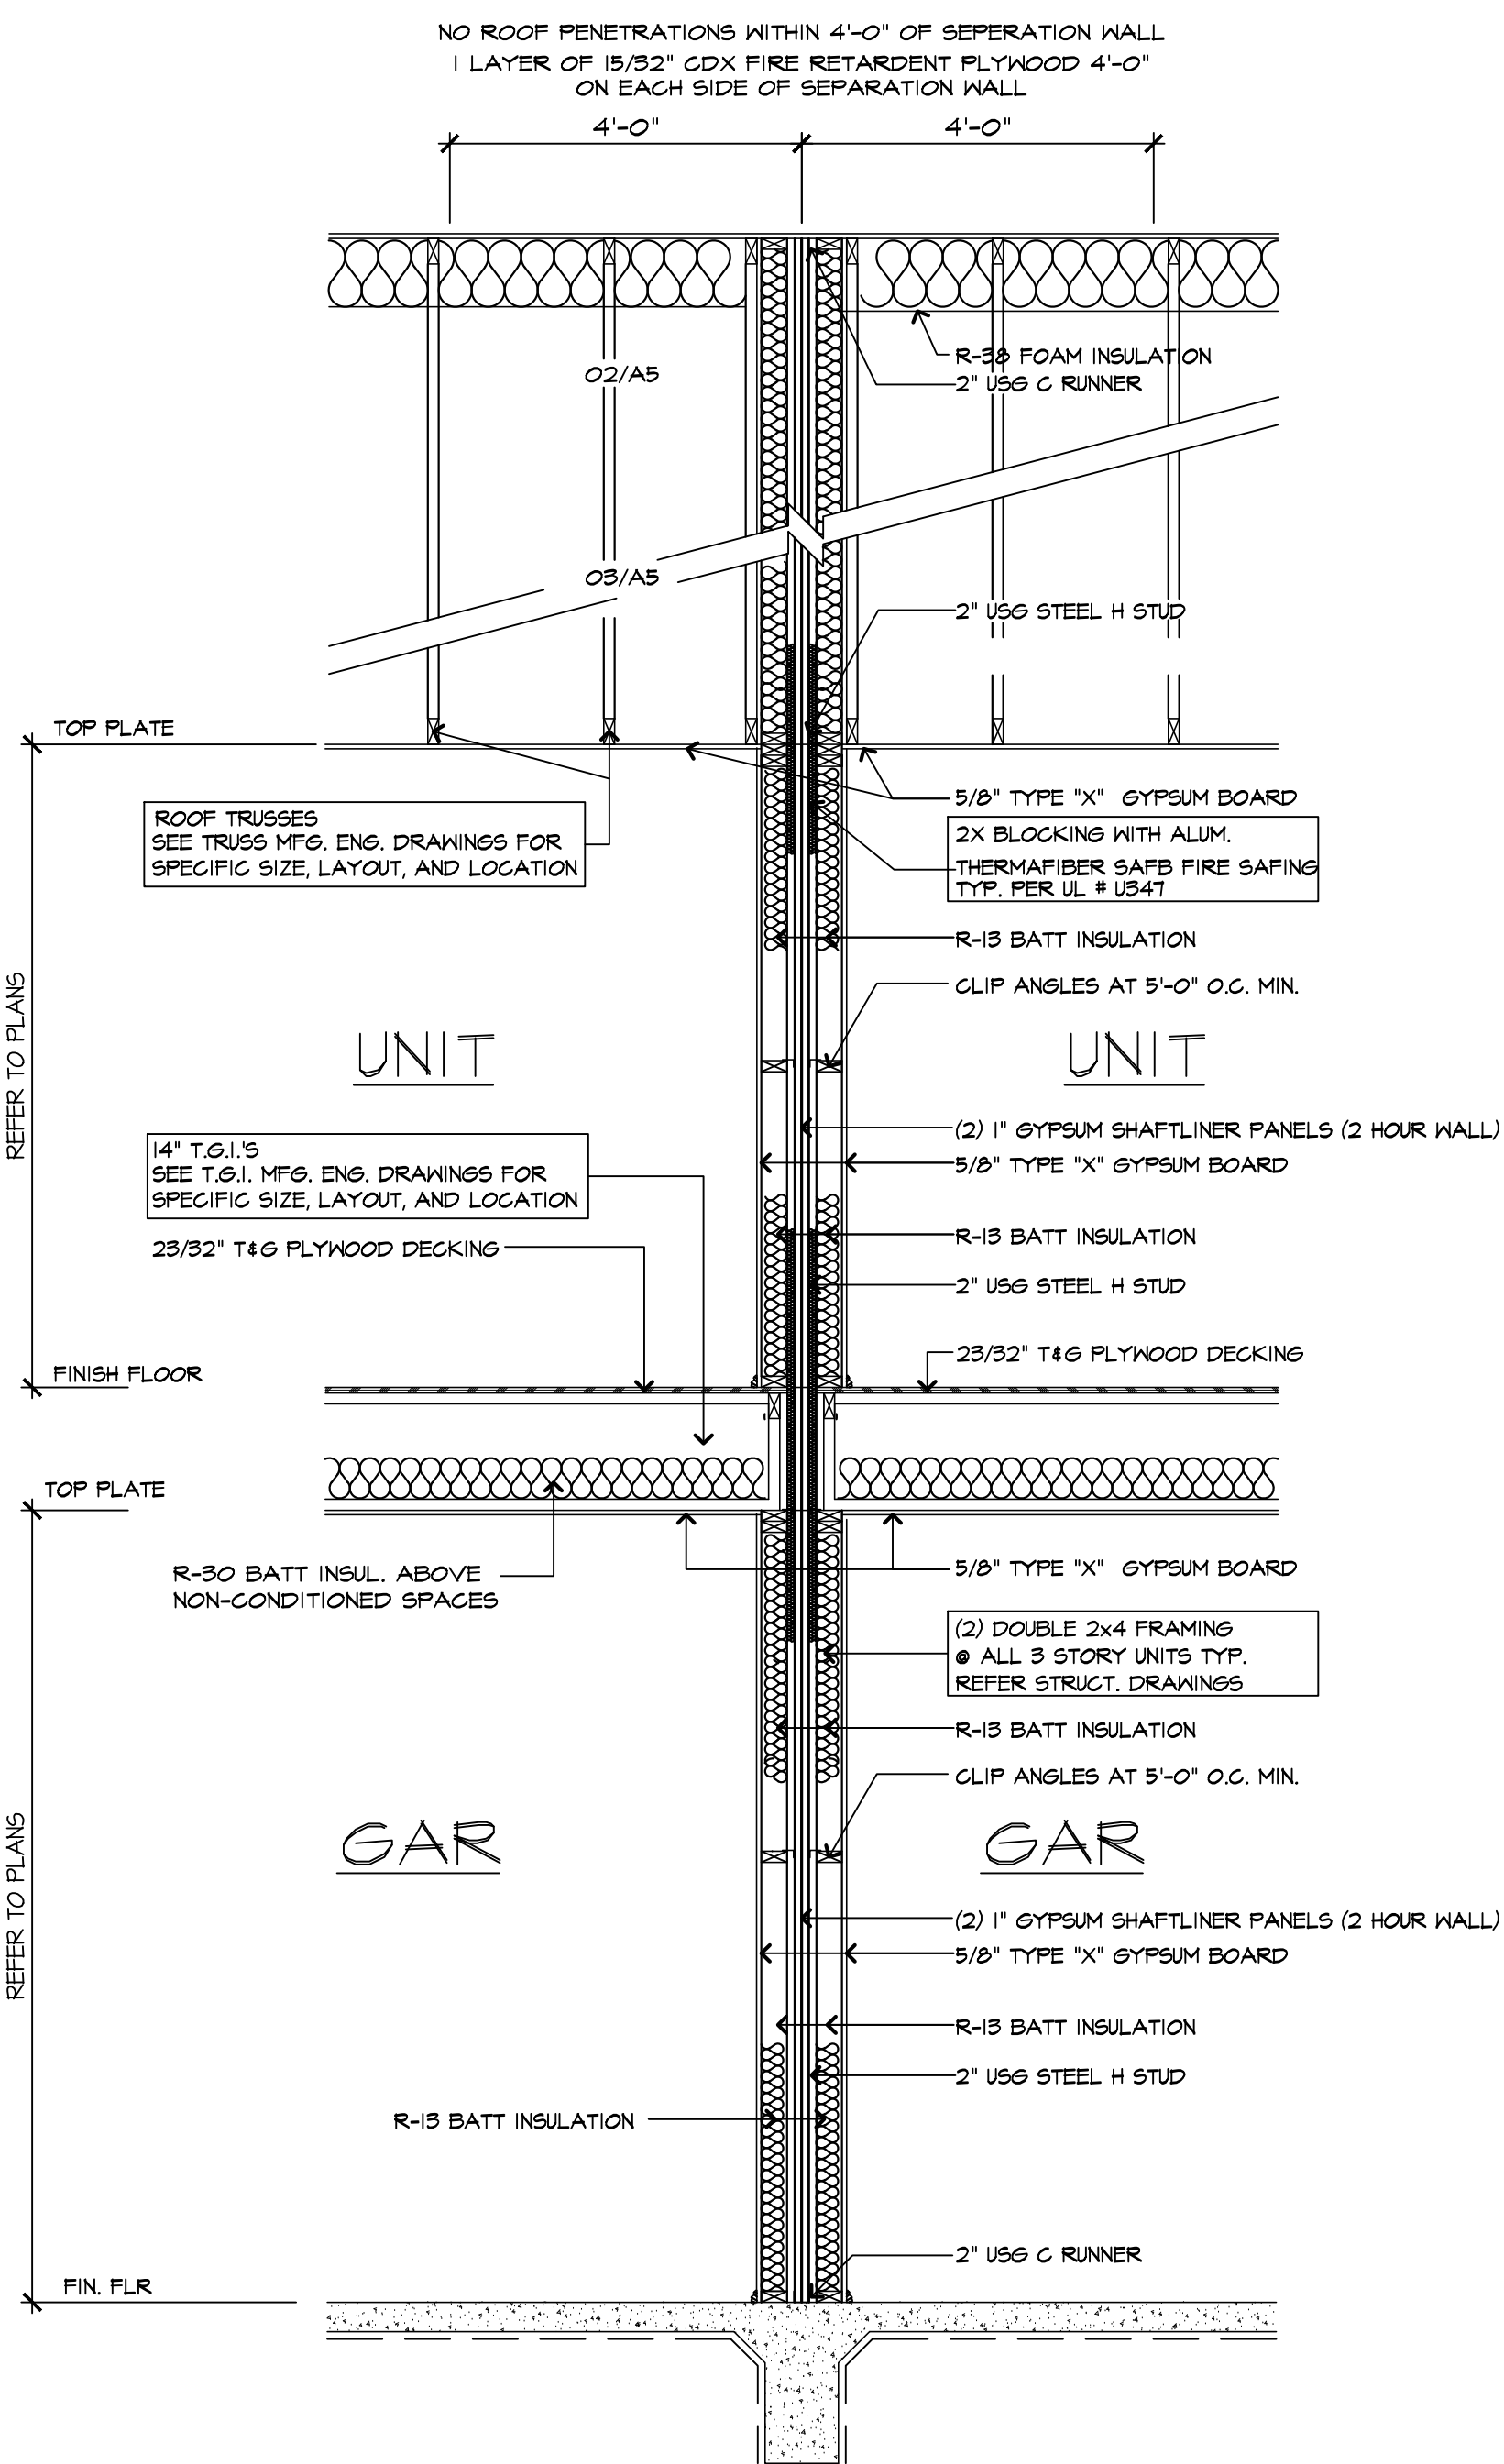

02 Typ. Party Wall Section
SCALE: 1/2" = 1'-0" 2 HOUR RATING PER UL # U347
CONFIG B: STC 70

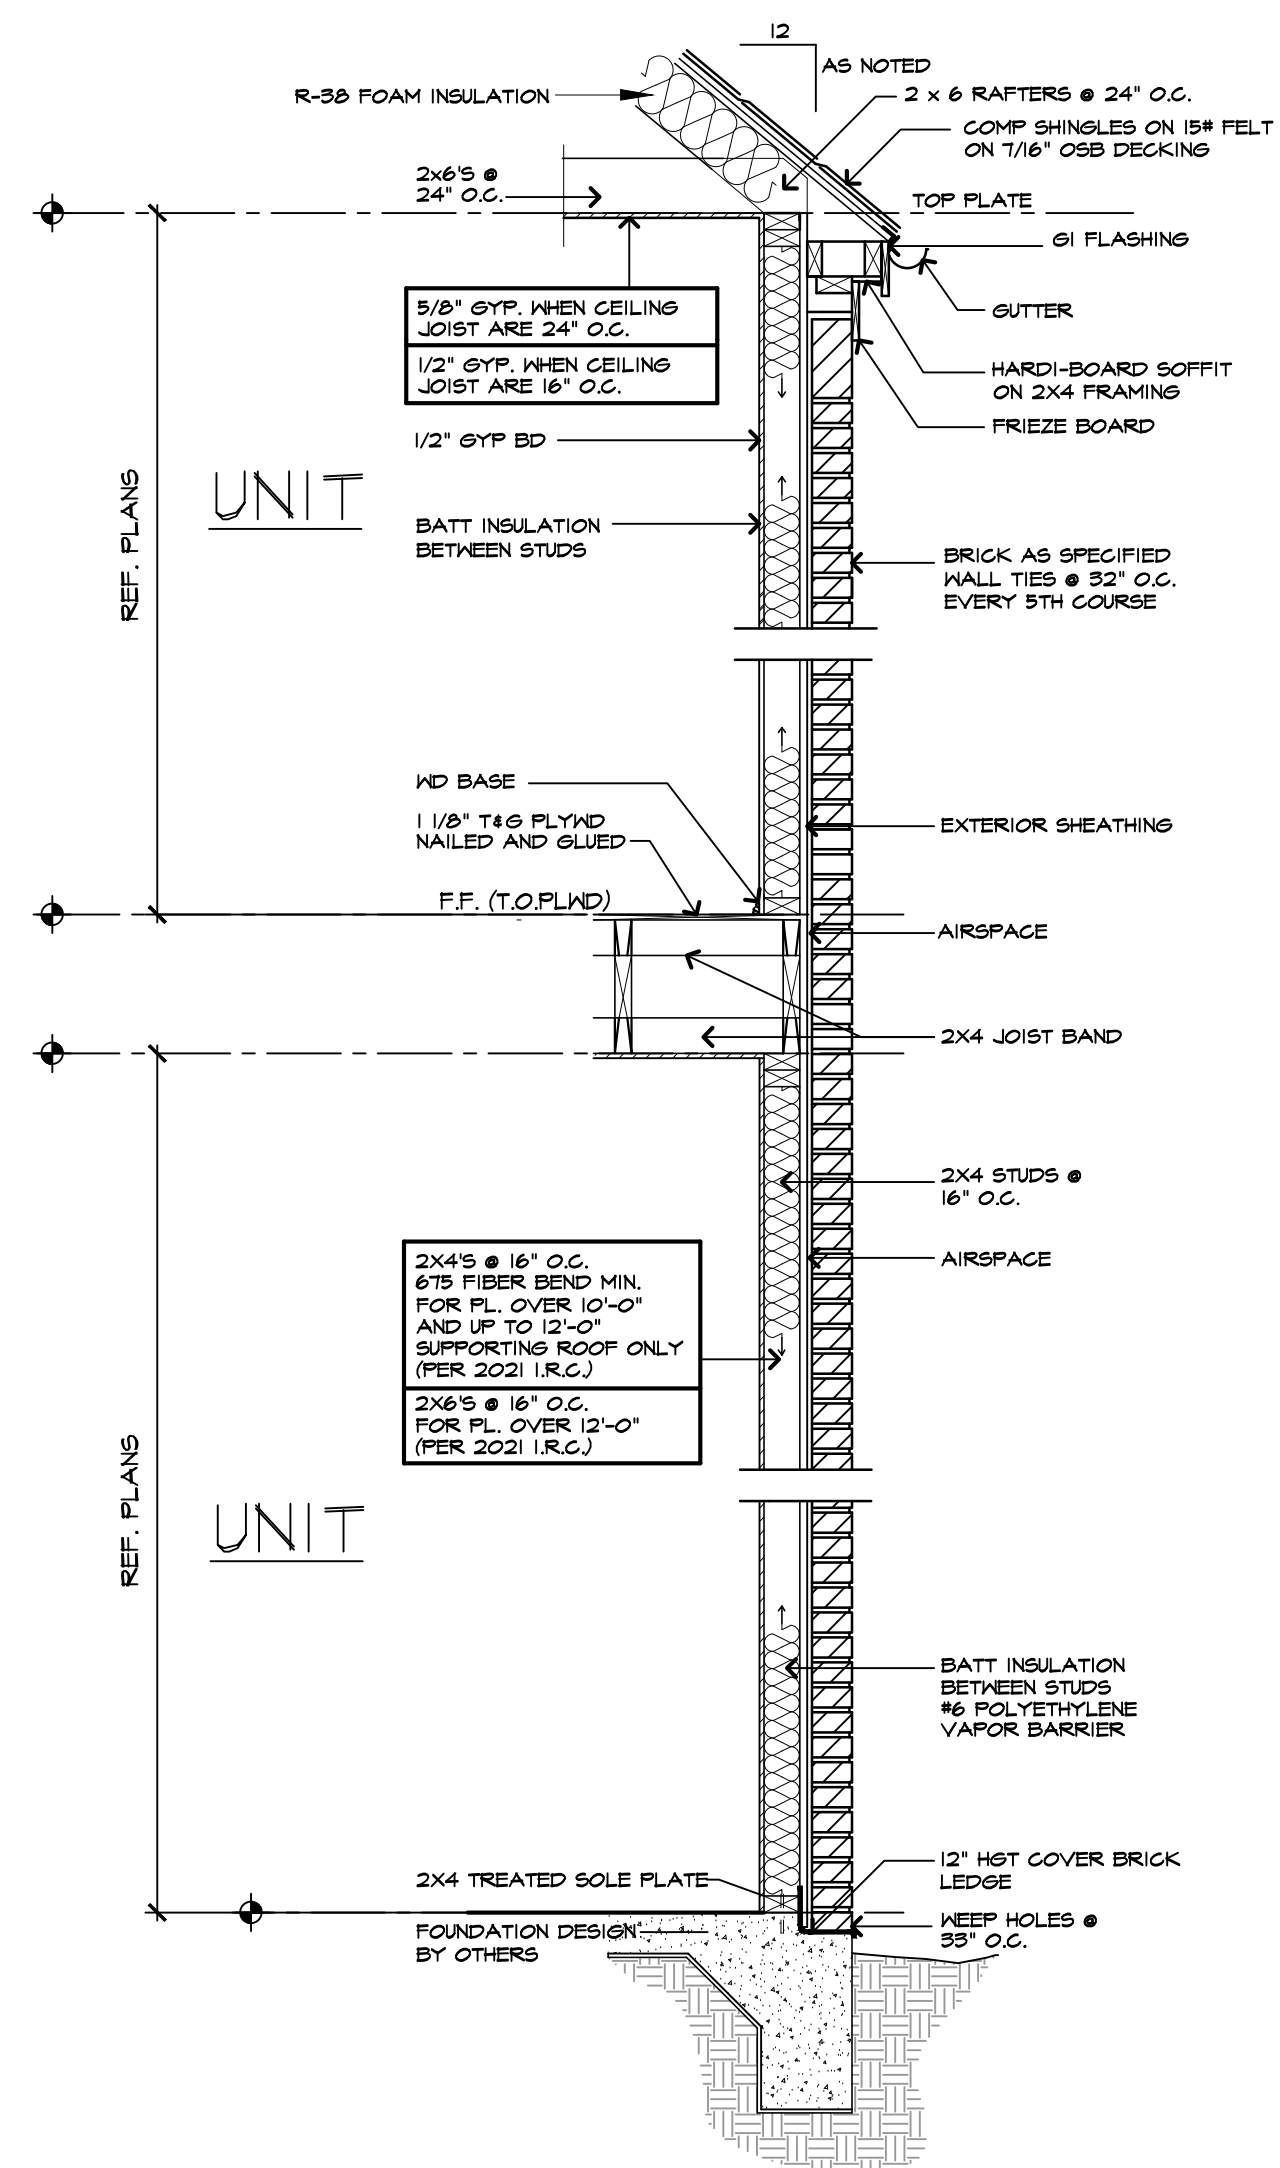


01 Typ. Exterior Wall Section
SCALE: 1/2" = 1'-0"

TYPICAL CONSTRUCTION ASSEMBLIES:

- A. TYPICAL ROOF CONSTRUCTION:
ASPHALT COMPOSITION ROOFING ON ROOF SHEATHING ON ROOF FRAMING MEMBERS AS NOTED ON FLOOR PLANS. CEILING: 5/8" GYPSUM BOARD.
- B. TYPICAL WALL CONSTRUCTION:
VENEER OR HARD-1 PANEL ON 5/8" INSULATING WALL SHEATHING ON 2x4 STUDS, 16" O.C. INTERIOR: 1/2" GYPSUM BOARD.
- C. TYPICAL FRAME FLOOR CONSTRUCTION:
FINISH FLOORING ON 22/32" T&G PLYWOOD DECKING ON 16" DEEP FLOOR TRUSSES AS NOTED ON FLOOR PLANS. MAIN FLOOR CEILING: 5/8" GYPSUM BOARD.
- D. BASEMENT FLOOR CONSTRUCTION:
3 1/2" CONCRETE SLAB OVER 6 MIL. POLYETHYLENE VAPOR BARRIER OVER 4" MINIMUM GRANULAR FILL.
- E. PLEASE SEE EXTERIOR ELEVATIONS FOR ALL FINISHITRATION LOCATIONS

DATE 11/8/24
Red Line
NAME
REVISIONS
1/17/25
2/26/25


Glenwick Drive SF/A
JGH LLC/JG Residential Properties, LLC
4328-30 Glenwick Drive
Lot 5 Block 15 of Highland Park HS Add. Dallas, TX

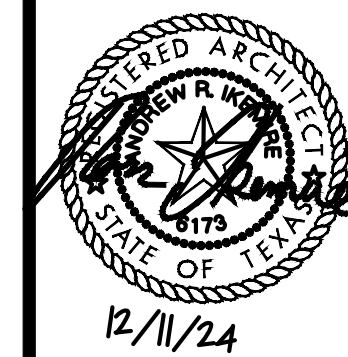

IKEMIRE ARCHITECTS, LLC
ARCHITECTURE PLANNING
16660 DALLAS PKWY. SUITE 2900 DALLAS, TX 75248-2488
972-248-1557
972-248-2486

A7

8 of 13
JOB #224045

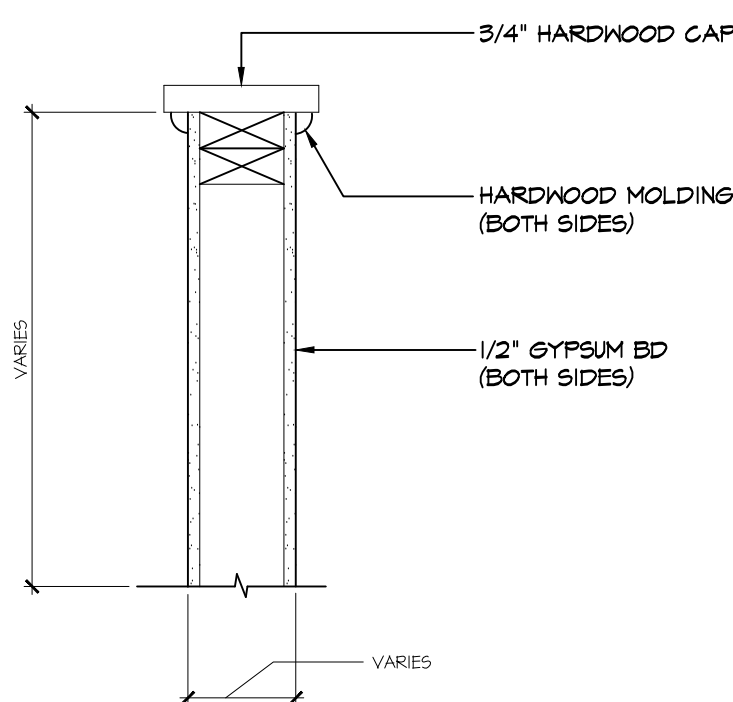

07 Typ. Low Wall Detail
SCALE: 1 1/2" = 1'-0"

HANDRAILS SHALL NOT BE LESS THAN 34" OR MORE THAN 38" IN HEIGHT ABOVE THE STAIR NOSING.
HANDRAILS SHALL BE CONTINUOUS PER FLIGHT OF STAIRS.
HANDRAILS SHALL BE 1 1/2" CLEAR OF ALL ADJACENT FINISH MATERIALS AND ENDS SHALL RETURN TO WALL OR TERMINATE 1 1/4"-2" IN CROSS SECTIONAL DIMENSION, OR APPROVED EQUIVALENT, IN NEEL POSTS OR SAFE TERMINALS. HANDRAILS SHALL BE AND BE SMOOTH WITH NO SHARP EDGES/CORNERS.

STAIR AND RAILING SUPPLIER INSTALLER SHALL SATISFY ALL BUILDING DEPARTMENT APPROVAL REQUIREMENTS FOR THE PRODUCTS THEY PROVIDE OR INSTALL.


THE HANDRAIL CONSTRUCTION SHALL BE ABLE TO RESIST A LOAD OF 200 LBS APPLIED IN ANY DIRECTION AT ANY POINT ALONG THE TOP RAIL.

GUARDRAILS SHALL NOT BE LESS THAN 36" IN HEIGHT.


OPEN RAILS SHALL HAVE INTERMEDIATE RAILS OR AN ORNAMENTAL PATTERN SUCH THAT A 4" DIAMETER SPHERE CANNOT PASS THROUGH.

THE GUARDRAIL CONSTRUCTION SHALL BE ABLE TO RESIST A CONCENTRATED LOAD OF 200 LBS IN ANY DIRECTION


THE TRIANGULAR OPENINGS AT STAIR TREAD, RISER, & BOTTOM SHALL BE SUCH THAT A 6" DIAMETER SPHERE CANNOT PASS THROUGH.

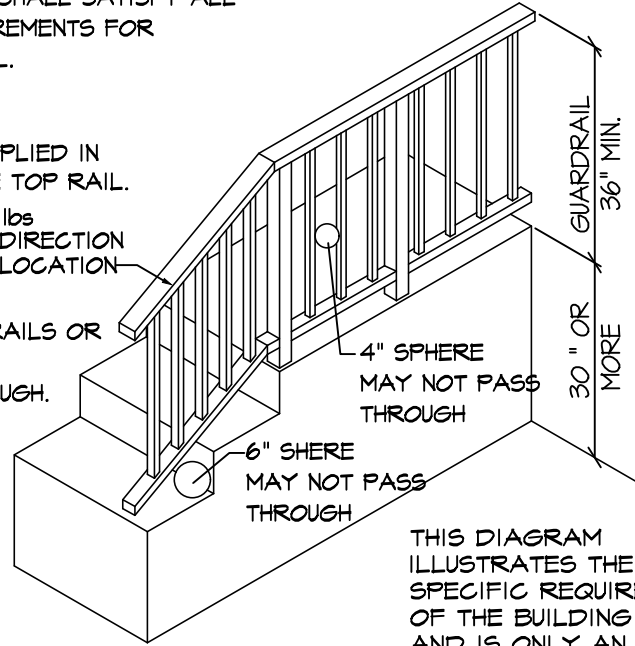


06 Handrail/Guardrail Code Data
SCALE: 1 1/2" = 1'-0" 02T06043.054_T2

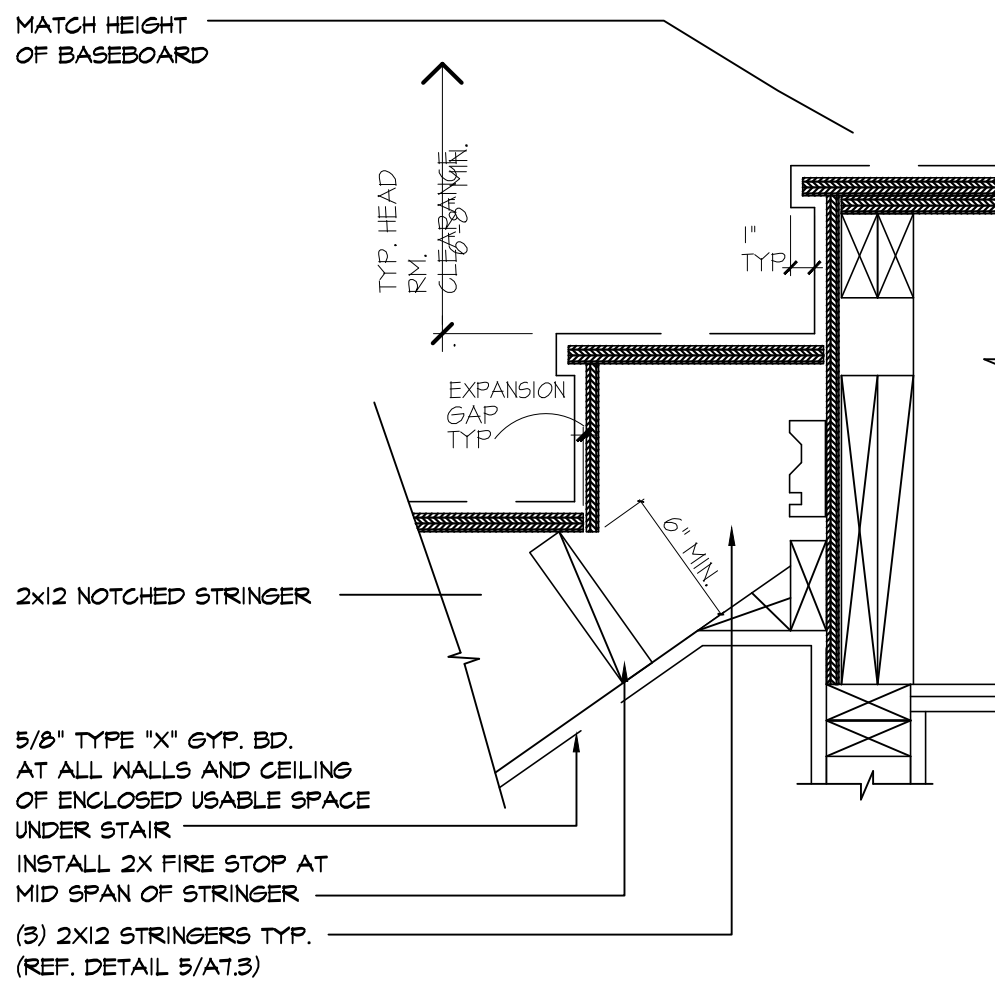


05 Stringer/Landing Detail
SCALE: 1 1/2" = 1'-0" 02T06043.054_T3

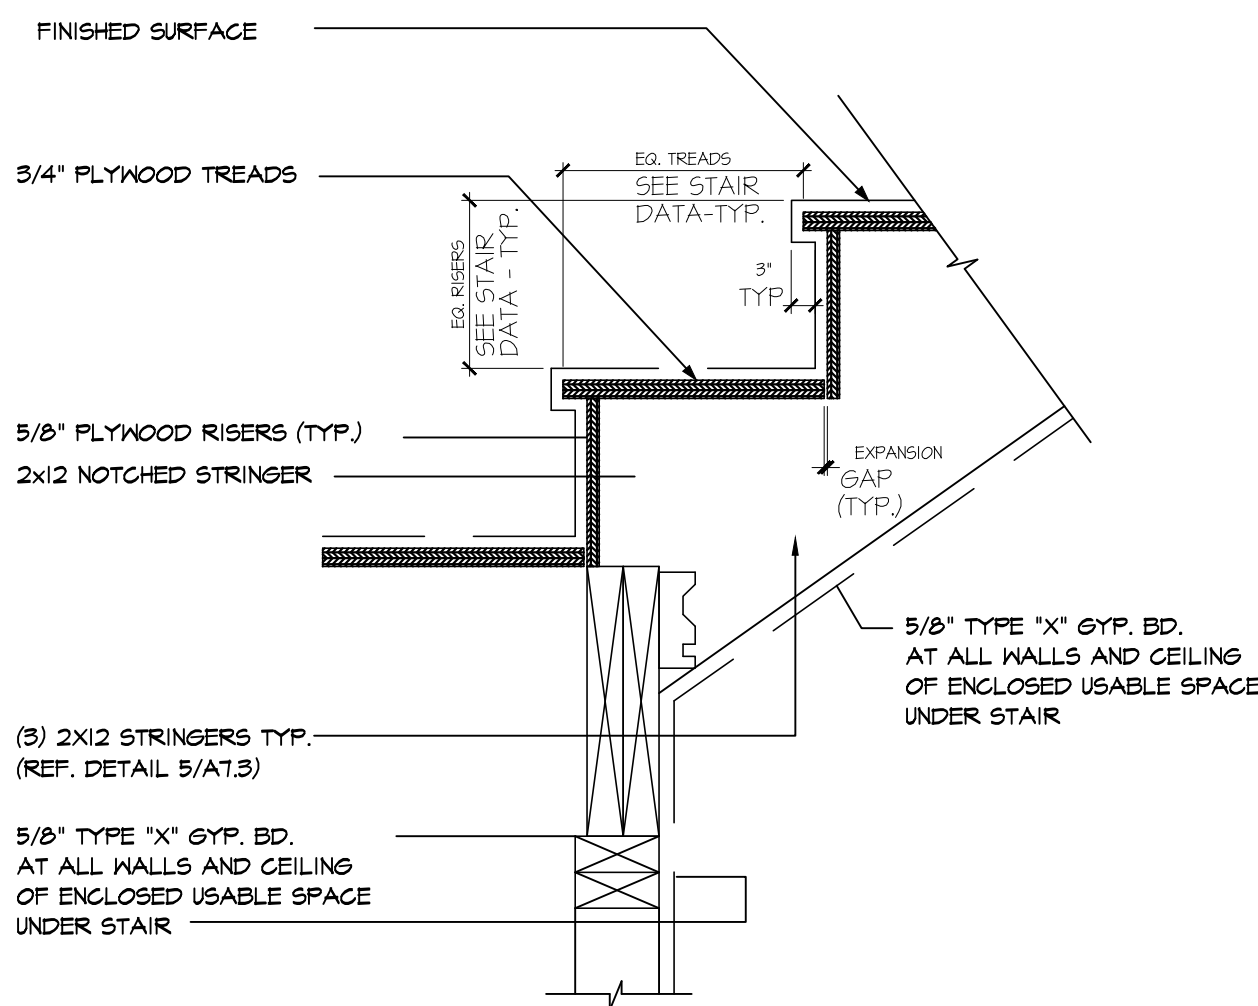


04 Landing/Stringer Detail
SCALE: 1 1/2" = 1'-0" 02T06043.054_T4

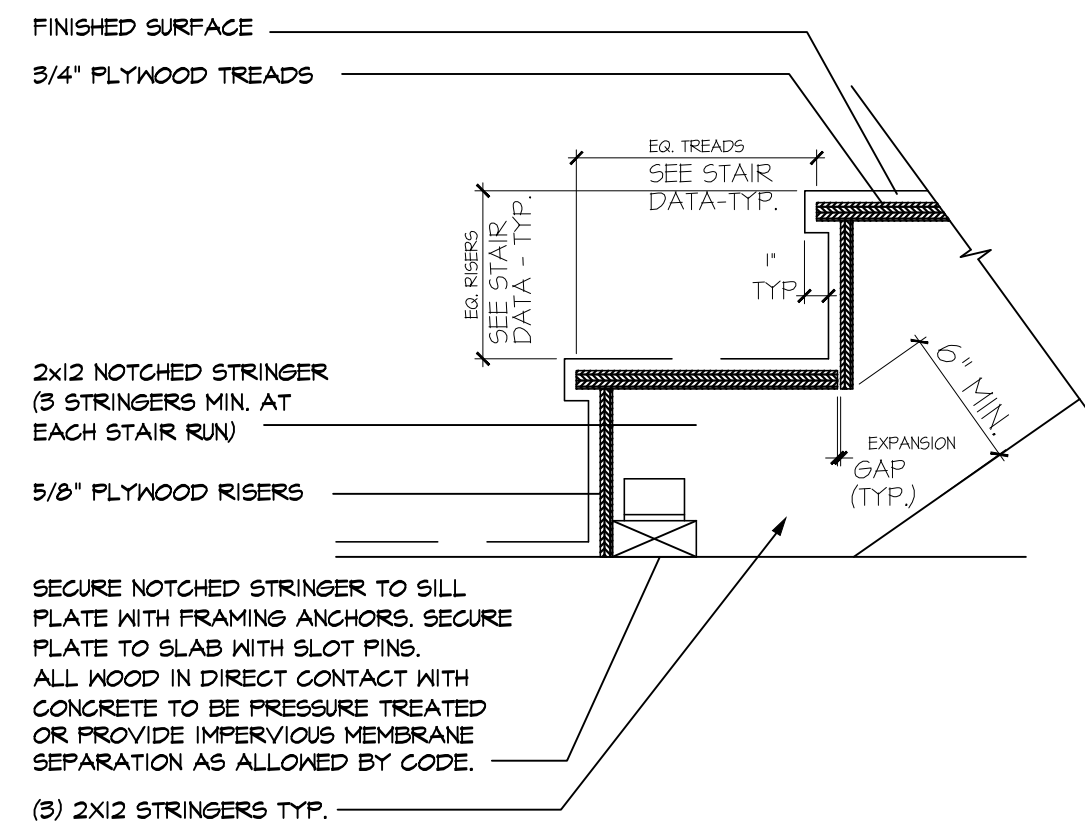

03 Floor/Stringer Detail
SCALE: 1 1/2" = 1'-0" 02T06043.054_T5

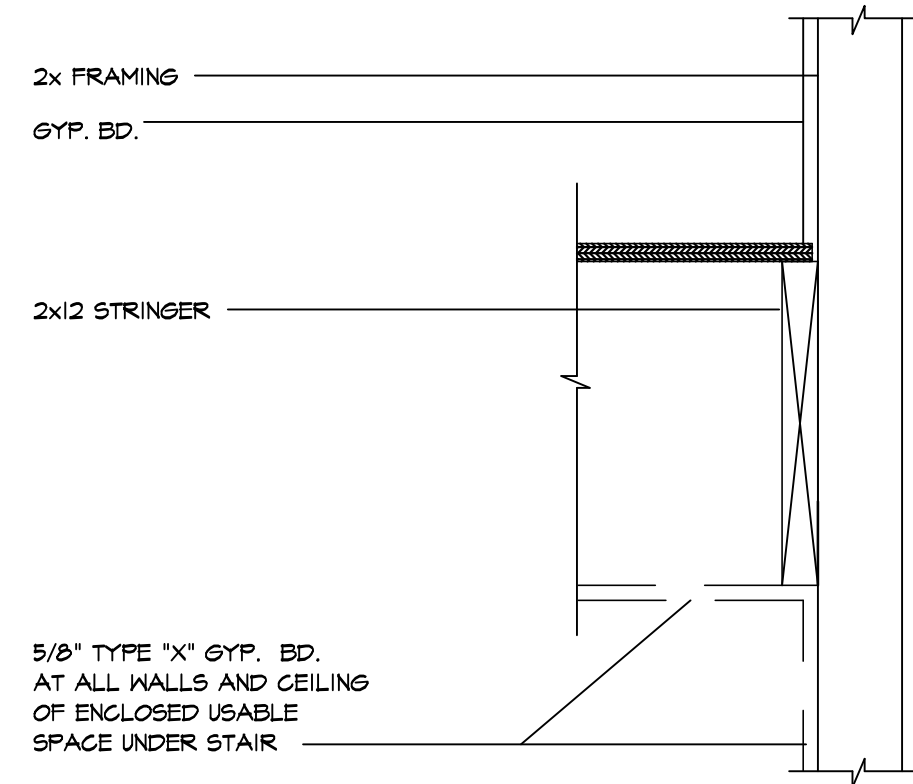

02 Stringer/Wall Detail
SCALE: 1 1/2" = 1'-0" 02T06043.054_T6

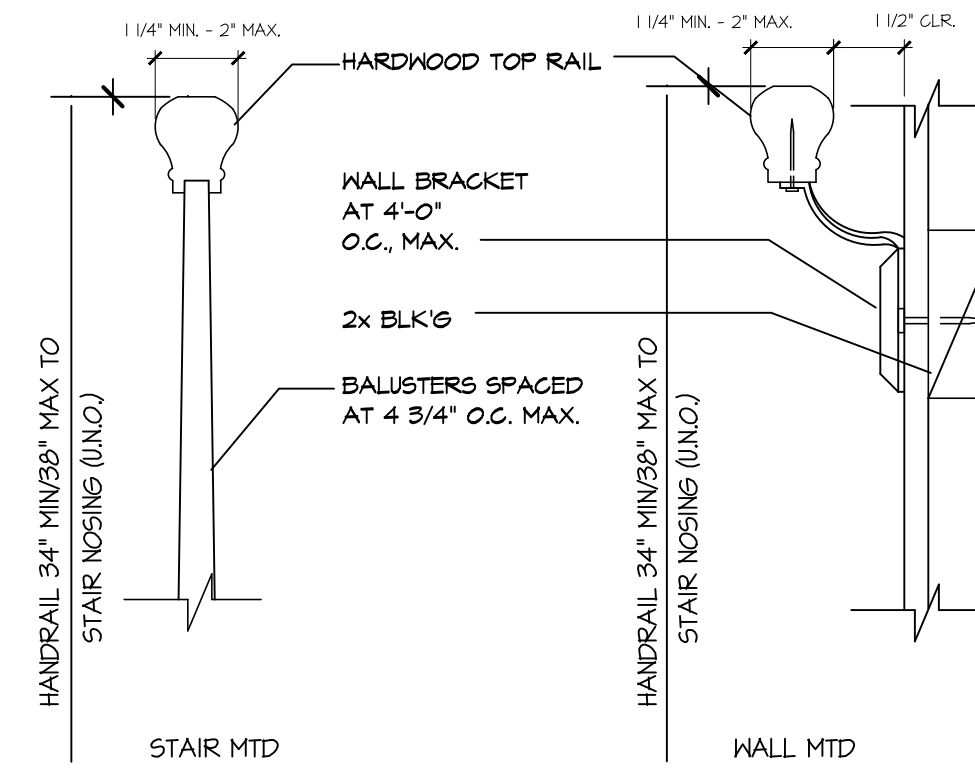

01 Handrail Detail
SCALE: 1 1/2" = 1'-0" 02T06043.054_T7

DATE 11/8/24
Red Line
NAME
REVISIONS
1/17/25
2/26/25



Glenwick Drive SF/A
JGH LLC/JG Residential Properties, LLC
4328-30 Glenwick Drive
Lot 5 Block 15 of Highland Park HS Add. Dallas, TX




IKEMIRE ARCHITECTS, LLC
ARCHITECTURE PLANNING INTERIORS
16660 DALLAS PKWY. SUITE 2900 DALLAS, TX 75248-2486
972-248-2486 FAX 972-248-1557

A8


9 of 13
JOB #224045

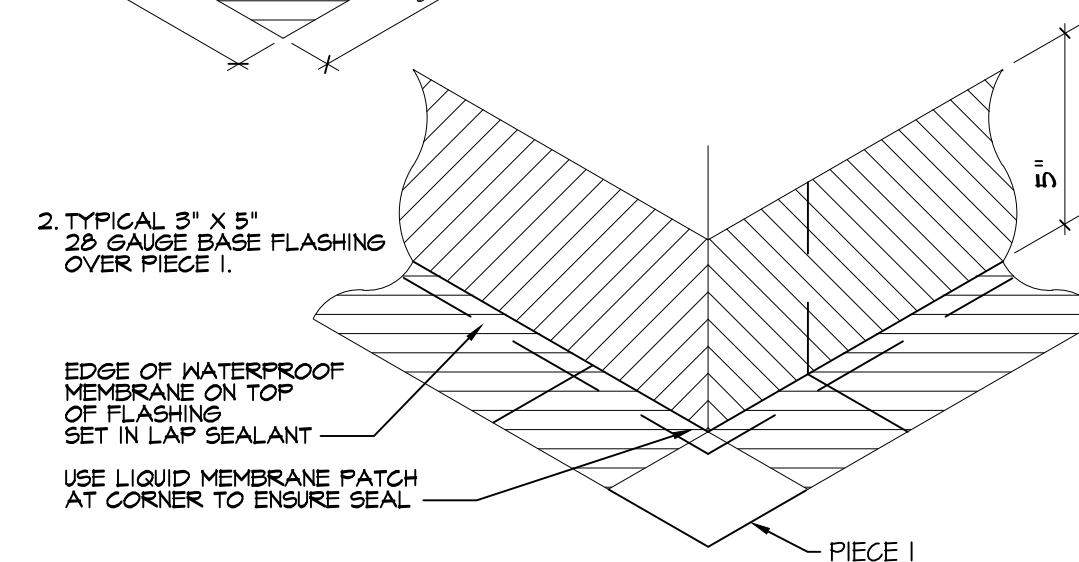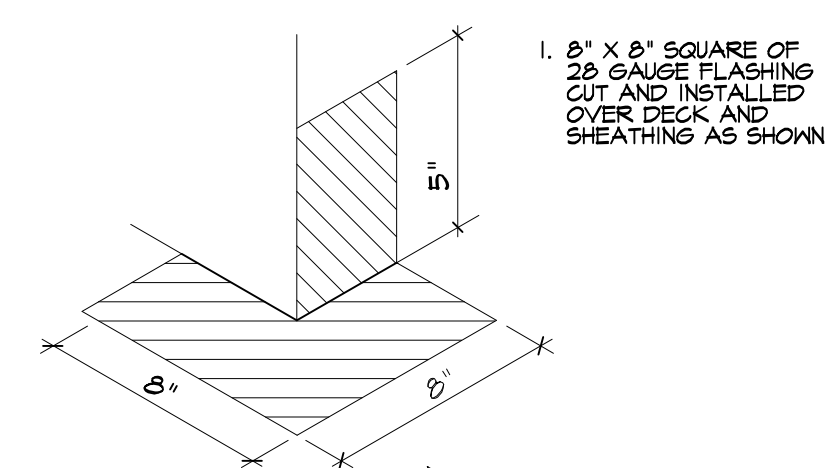


08 Flashing Detail at Outside Crnr.
SCALE: 3" = 1'-0"

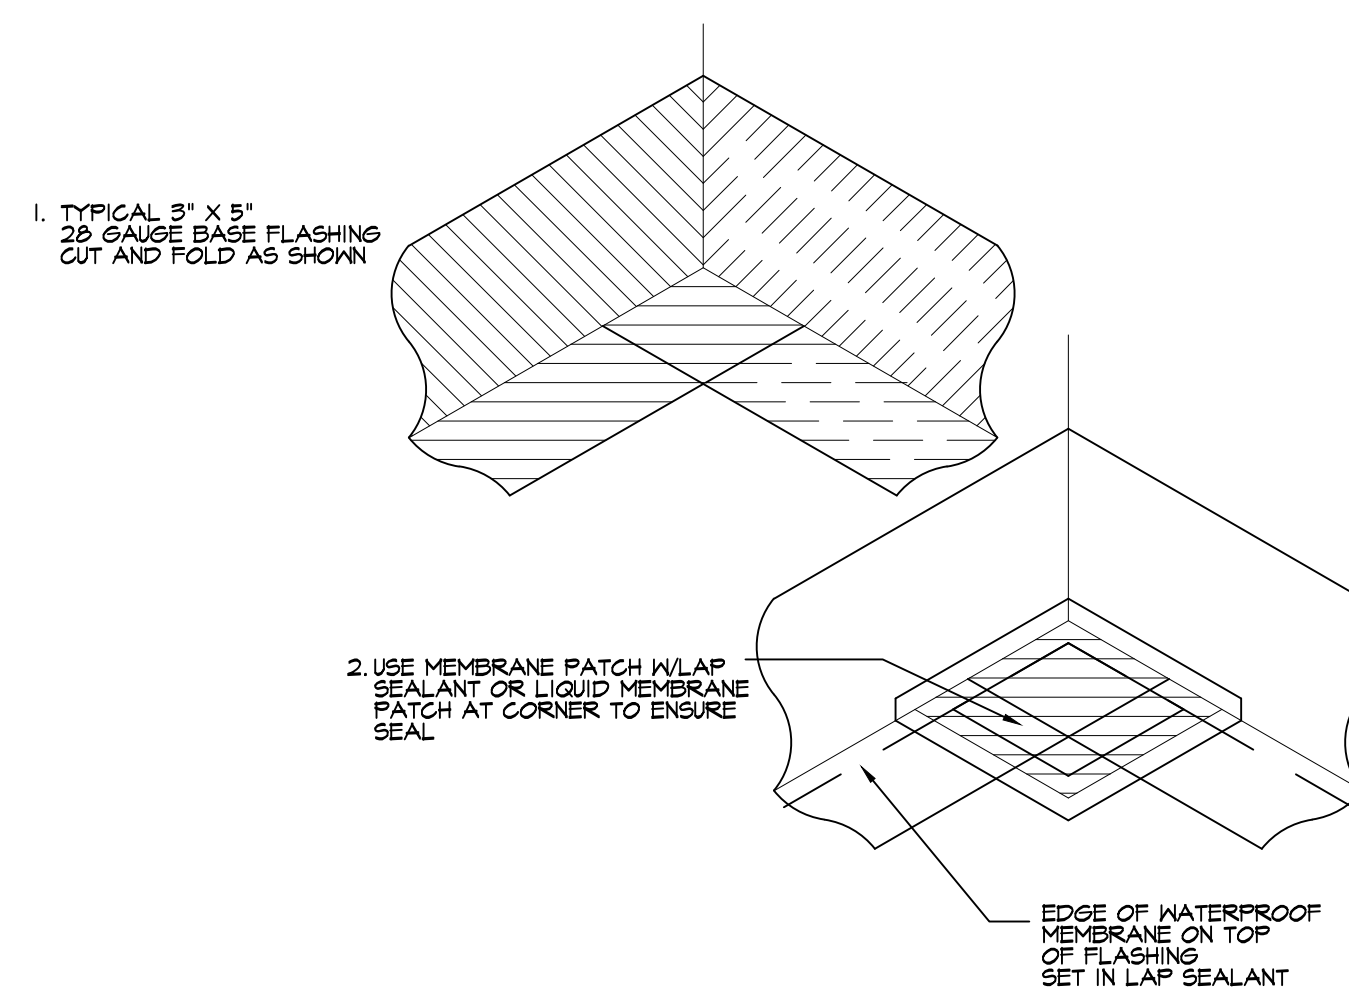


07 Flashing Detail at Inside Cnr.
SCALE: 3" = 1'-0"

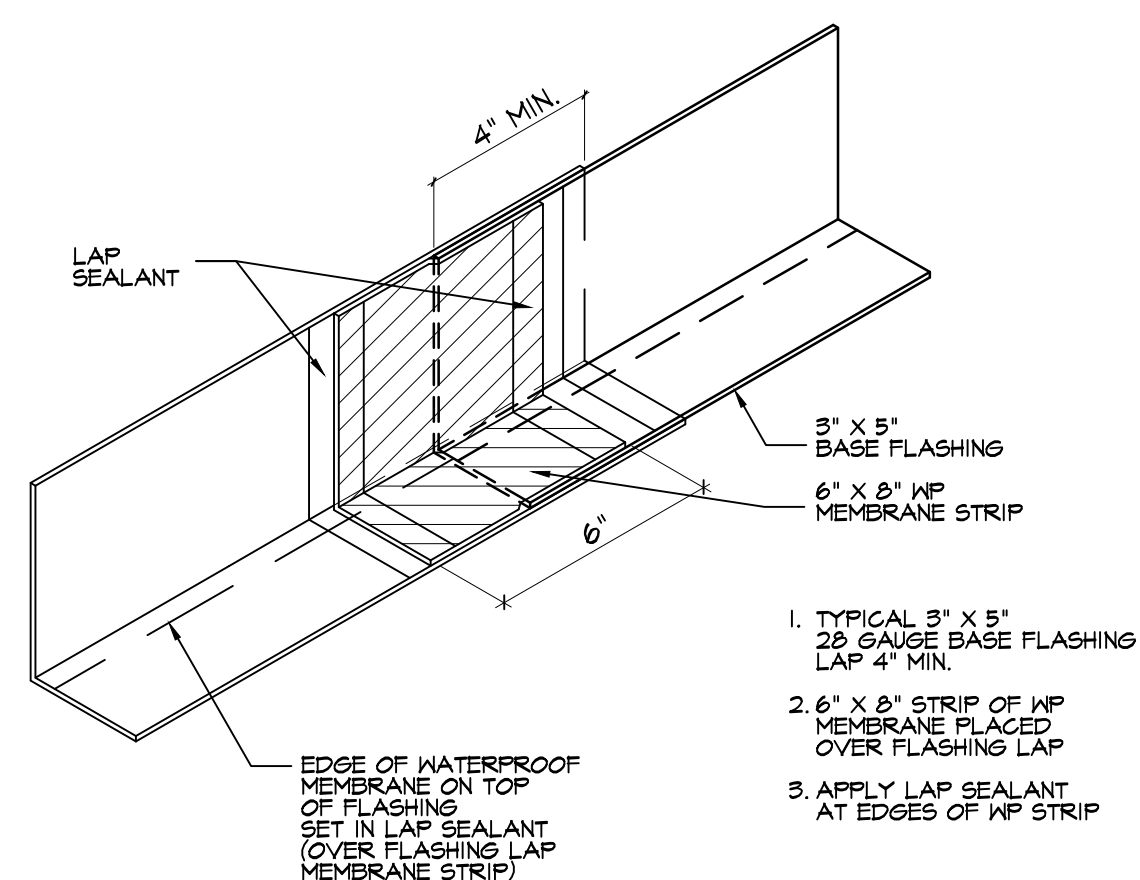


06 Flashing Lap
SCALE: 3" = 1'-0"

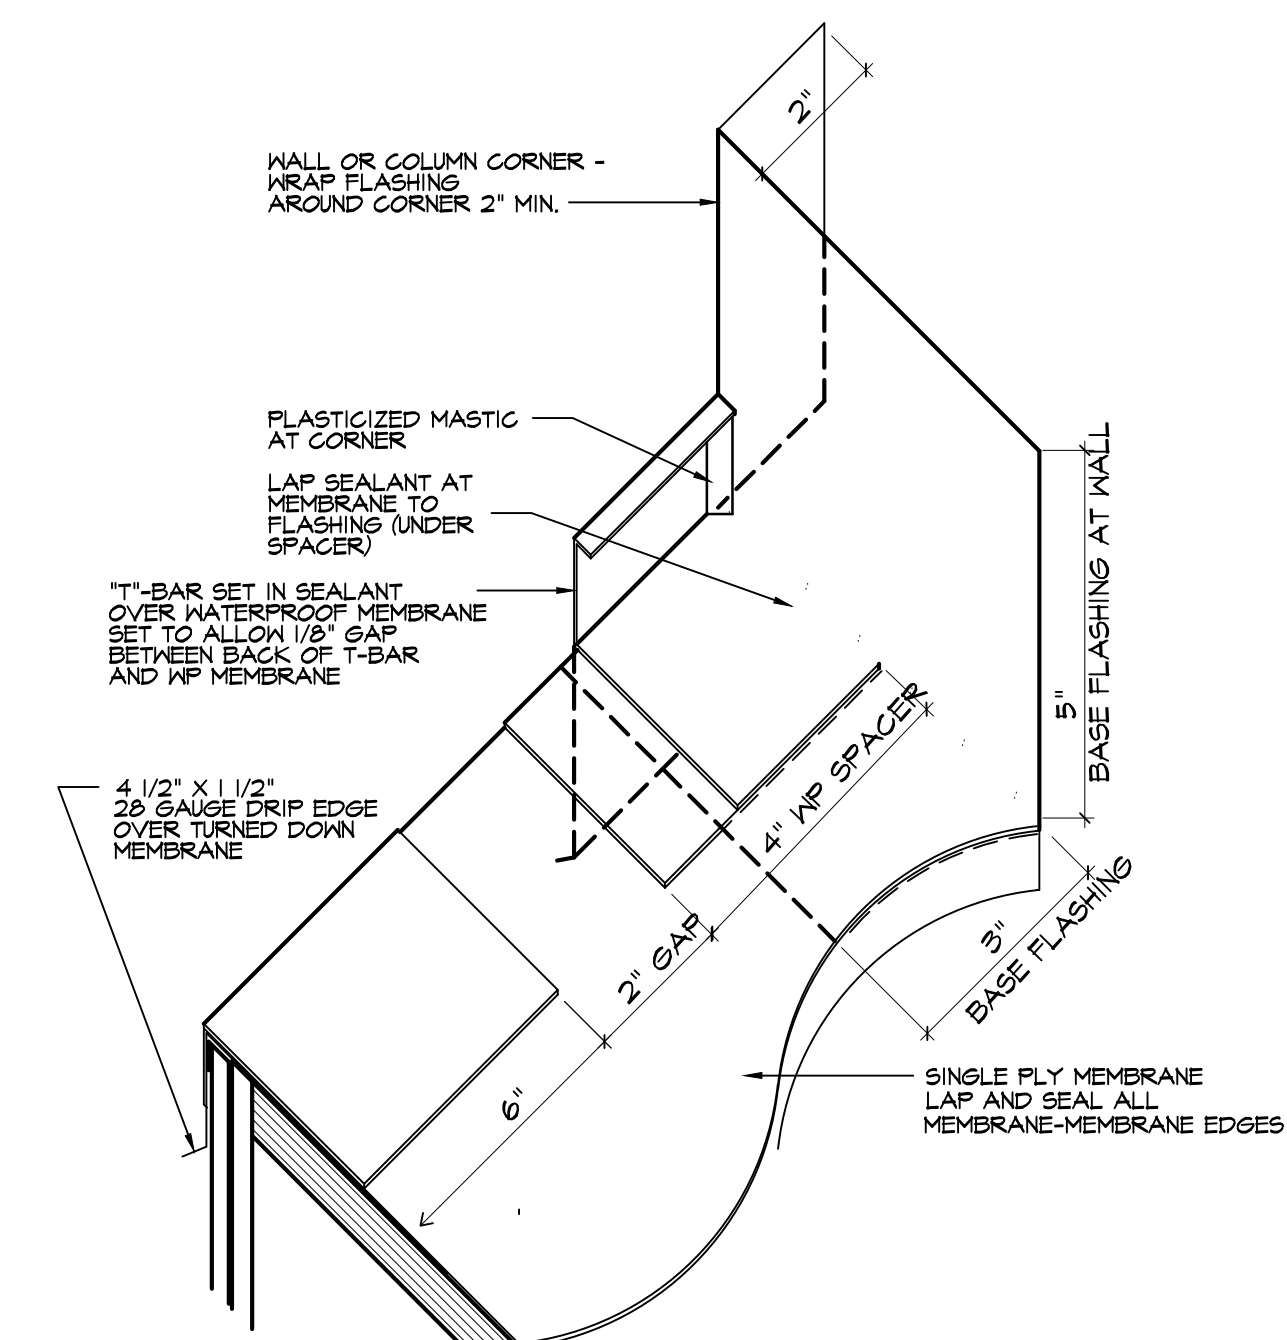


02 T Bar at Wall
SCALE: 6" = 1'-0"

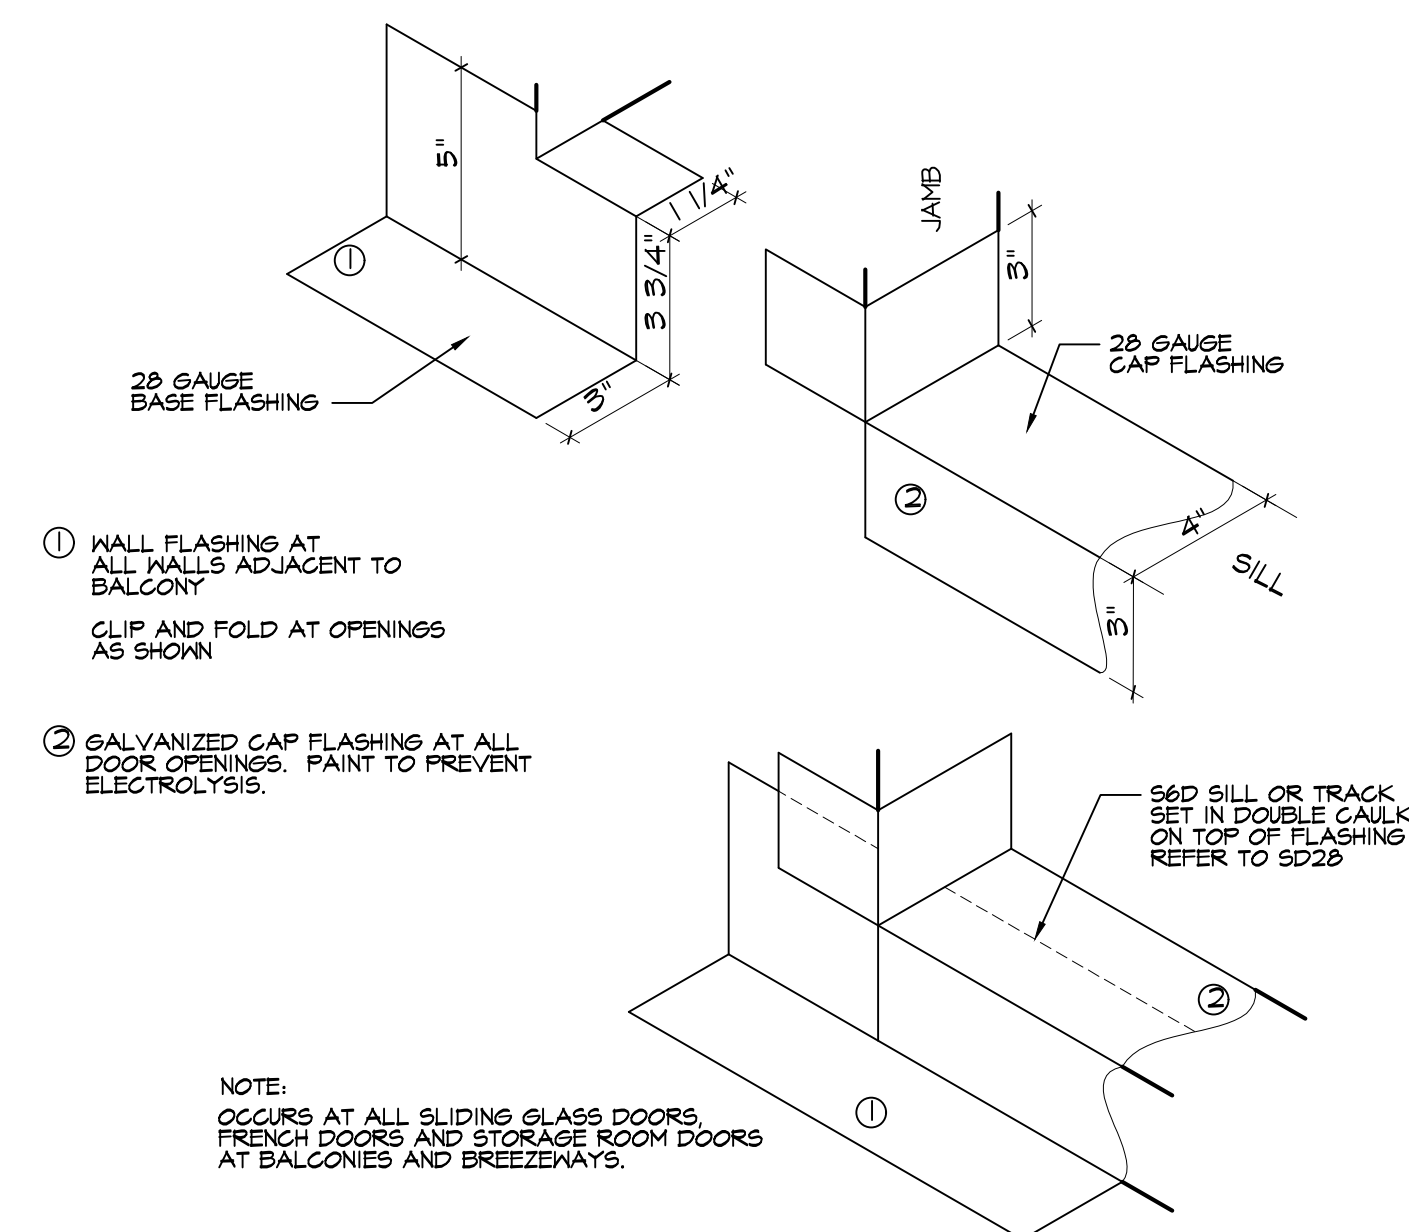

Flash'g at Door Openings

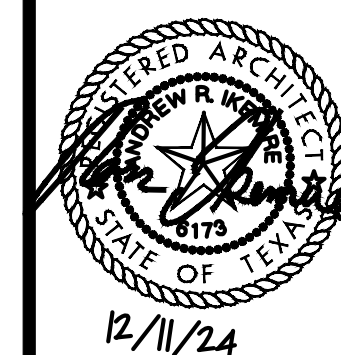

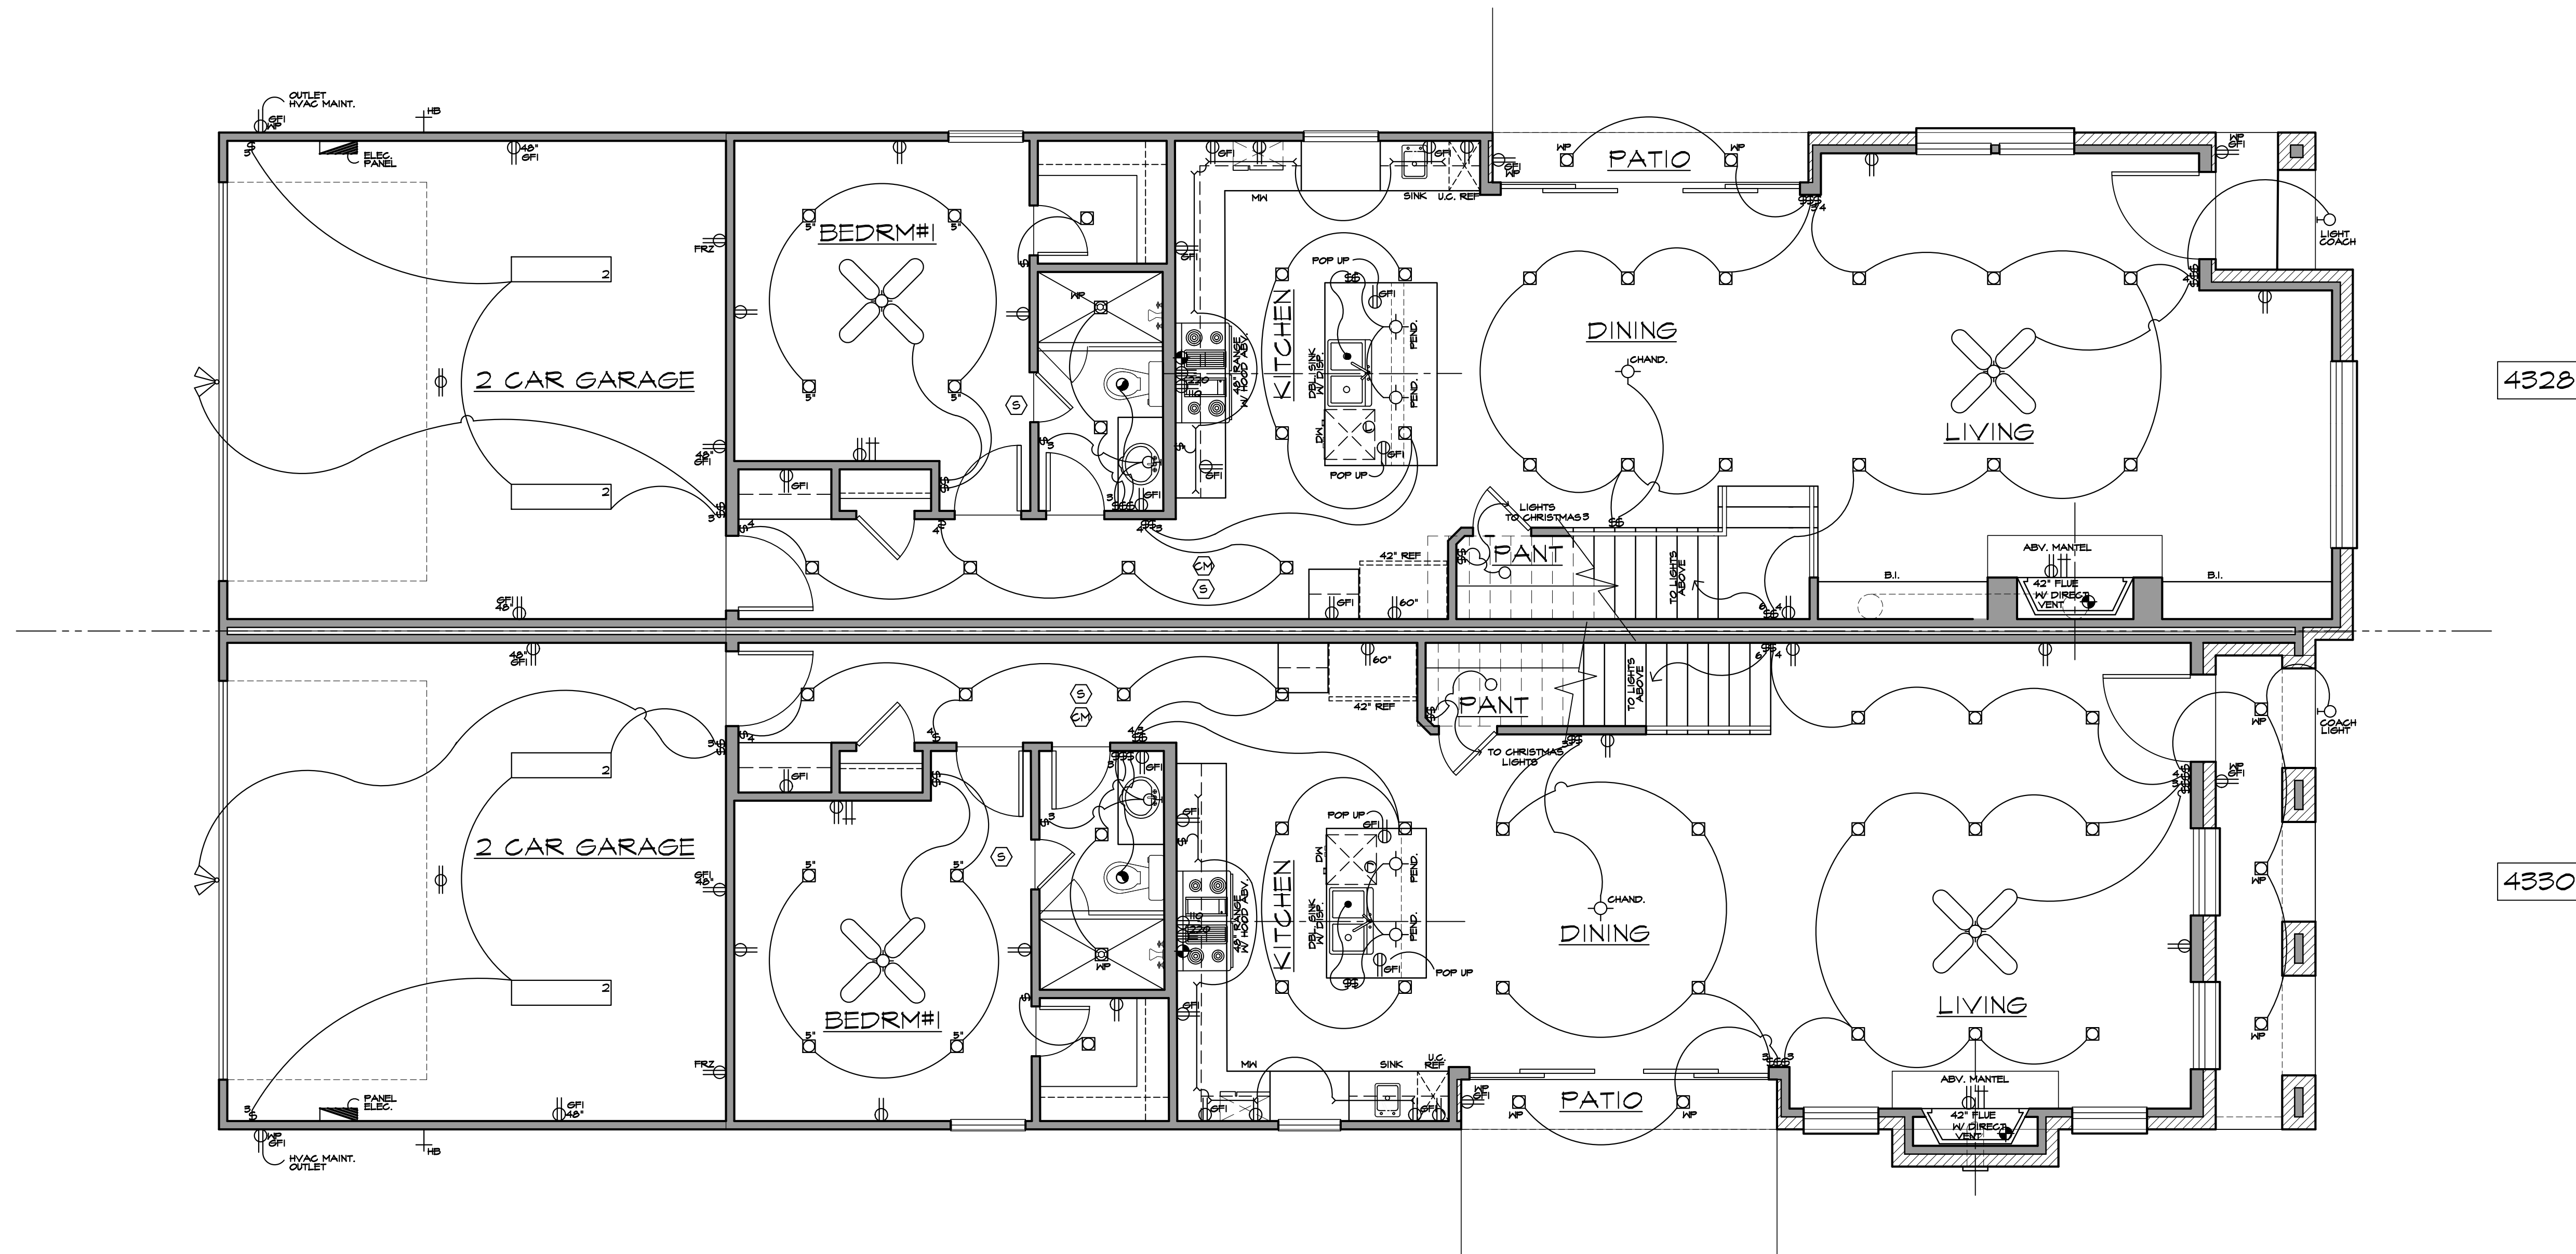

FIRST FLOOR ELECTRICAL PLAN

SCALE: 1/4" = 1'-0"


ELECTRICAL SYMBOLS			
	110V. DUPLEX		FLOOD LIGHT
	110V. DUPLEX SWITCH AT TOP ONLY		SMOKE DETECTOR
	220V. OUTLET		CARBON MONOXIDE DETECTOR
	WATERPROOF OUTLET		RECESS EYEBALL
	GROUND FAULT		CEILING MOUNTED FIXTURE
	110V. CEILING OUTLET		WALL BRACKET
	110V. FLOOR OUTLET		RECESSED CAN FIXTURE
	SINGLE POLE SWITCH		PEND. LITE
	THREE WAY SWITCH		FLUORESCENT DRAWN TO SCALE
	DIMMER SWITCH		UNDER / OVER CABINET FLUORESCENT LITE
	110V. JUNCTION BOX		GAS OUTLET
	EXHAUST FAN		TELEVISION OUTLET
	DOORBELL		TELEPHONE OUTLET
	DOORBELL CHIME		SERVICE PANEL
	CLG. FAN W/ LIGHT FIXT.		GARAGE DOOR OPENER

NOTE: ADD OUTLETS AS REQUIRED BY 2020 NATIONAL ELECTRIC CODE.

DATE 11/8/24
Red Line
NAME
REVISIONS
11/17/25
5/1/25
Glenwick Drive SF/A
JGH, LLC/JG Residential Properties, LLC
4328-30 Glenwick Drive
Lot 5 Block 15 of Highland Park HS Add. Dallas, TX



IKEMIRE ARCHITECTS, LLC
ARCHITECTURE PLANNING INTERIORS
16660 DALLAS PKWY. SUITE 2900 DALLAS, TX 75248-2486 FAX 972-248-1557
972-248-2486

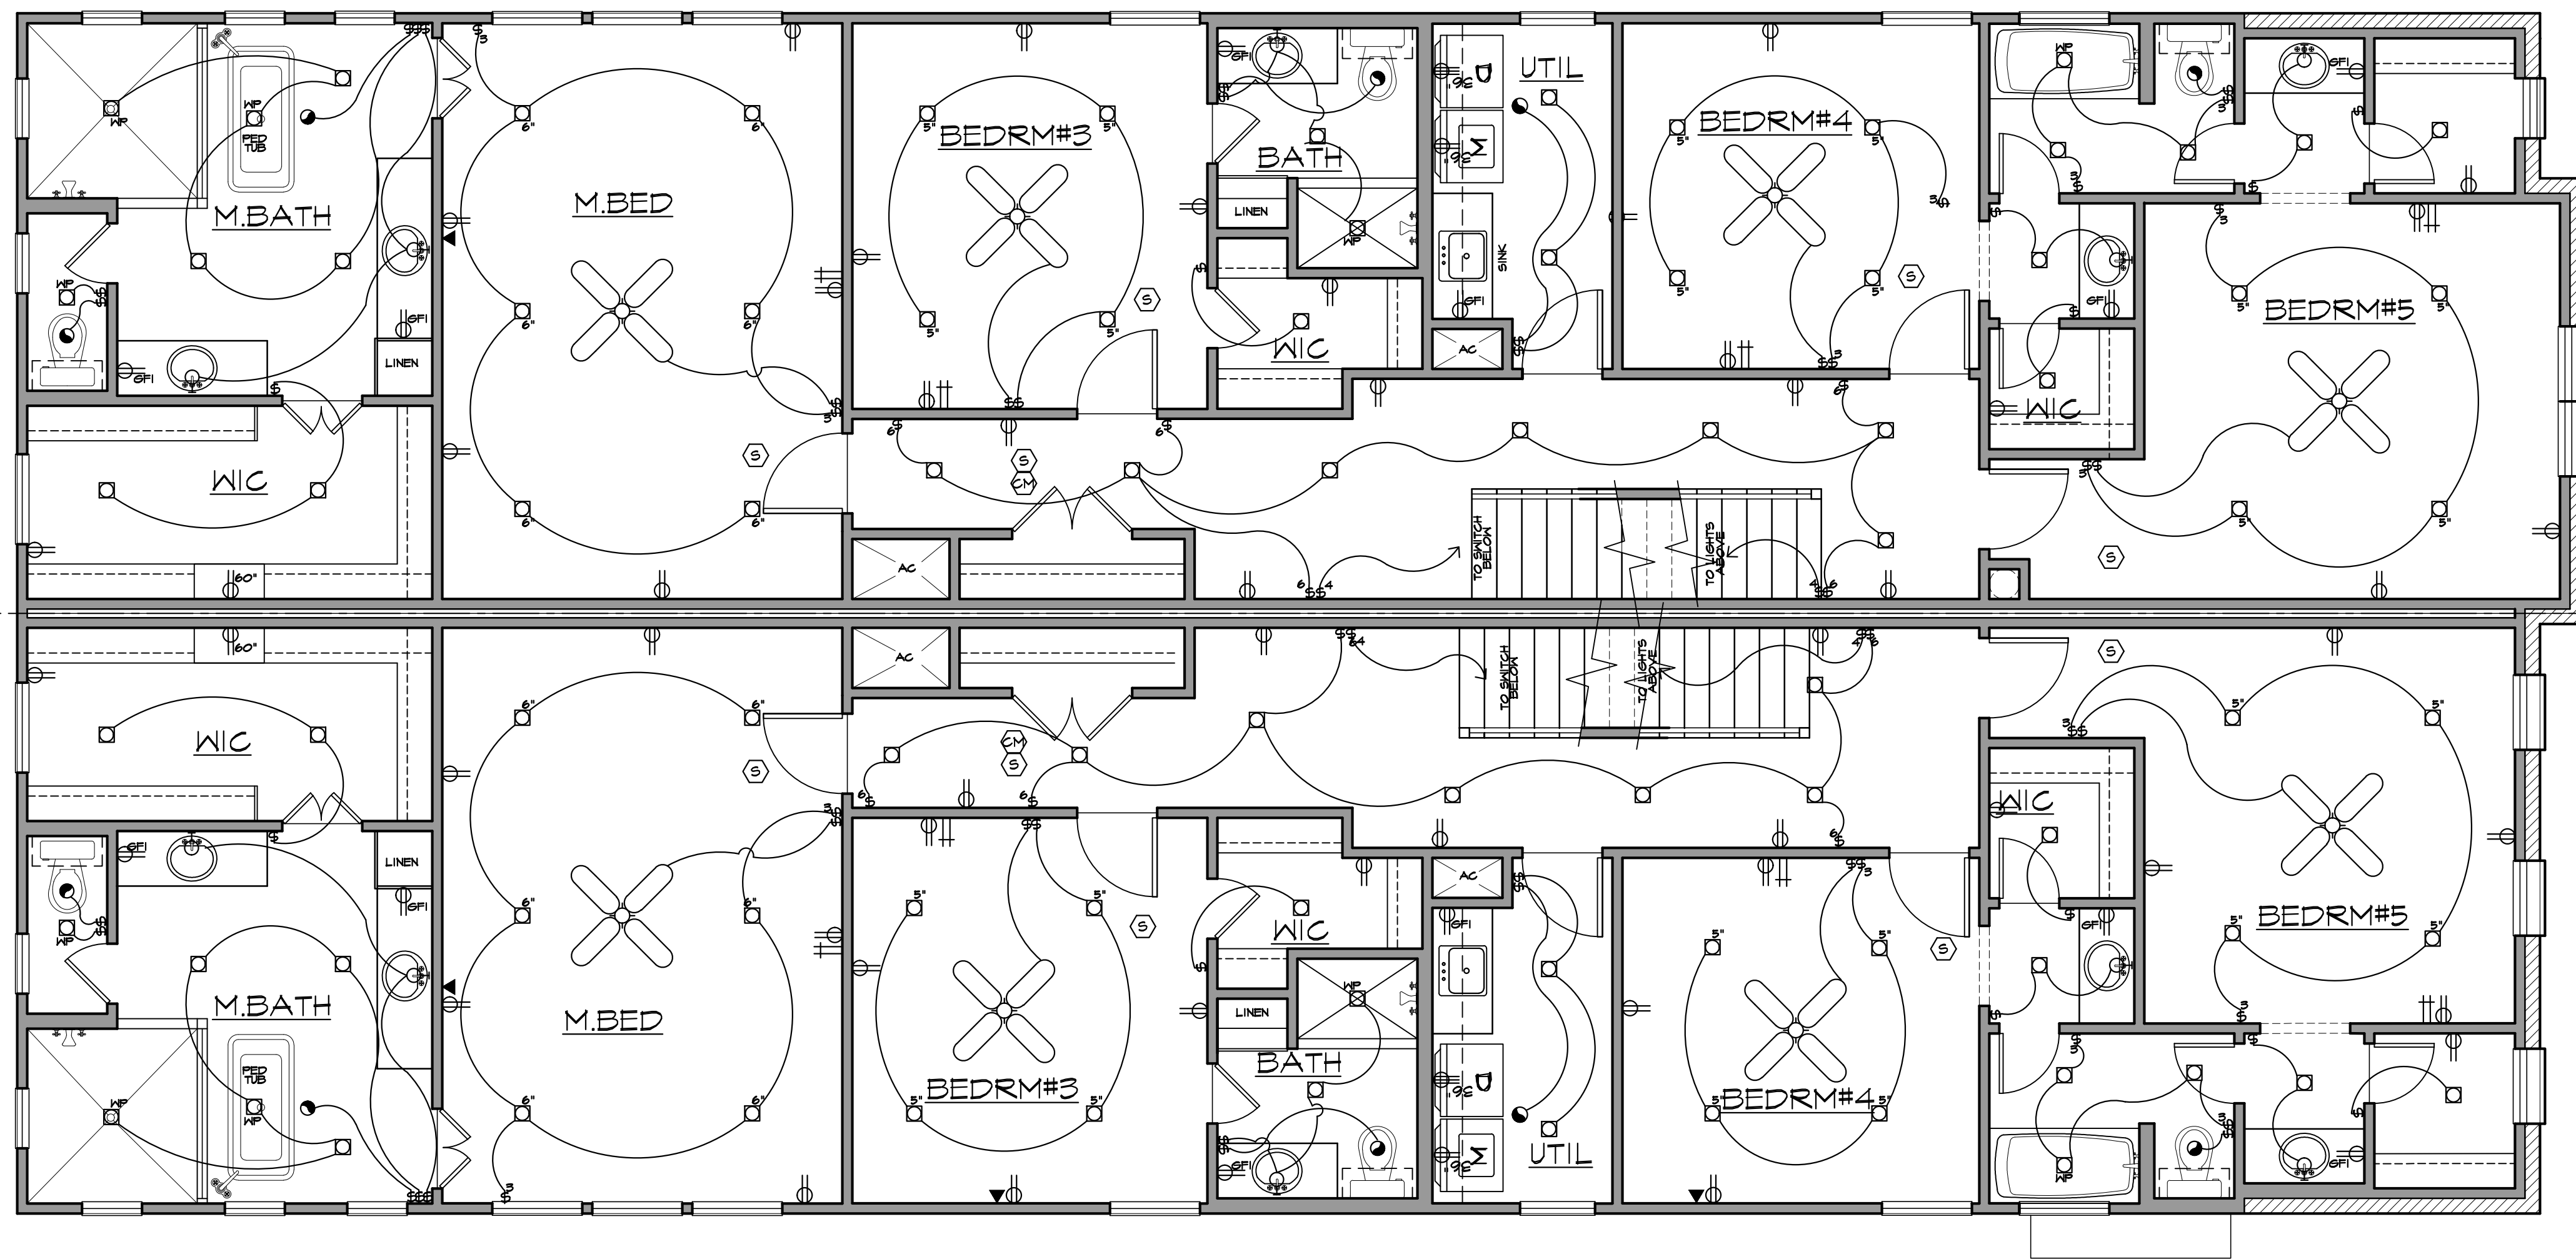

ELECTRICAL SYMBOLS			
	110V. DUPLEX		FLOOD LIGHT
	110V. DUPLEX SWITCH AT TOP ONLY		SMOKE DETECTOR
	220V. OUTLET		CARBON MONOXIDE DETECTOR
	WATERPROOF OUTLET		RECESS EYEBALL
	GROUND FAULT		CEILING MOUNTED FIXTURE
	110V. CEILING OUTLET		WALL BRACKET
	110V. FLOOR OUTLET		RECESSED CAN FIXTURE
	SINGLE POLE SWITCH		PEND. LITE
	THREE WAY SWITCH		FLUORESCENT DRAWN TO SCALE
	DIMMER SWITCH		UNDER / OVER CABINET FLUORESCENT LITE
	110V. JUNCTION BOX		GAS OUTLET
	EXHAUST FAN		TELEVISION OUTLET
	DOORBELL		TELEPHONE OUTLET
	DOORBELL CHIME		SERVICE PANEL
	CLG. FAN W/ LIGHT FIXT.		GARAGE DOOR OPENER

NOTE: ADD OUTLETS AS REQUIRED BY 2020 NATIONAL ELECTRIC CODE.

DATE 11/8/24
Red Line
NAME
REVISIONS
11/7/25
5/7/25
5/3/25
Glenwick Drive SF/A
JGH, LLC/JG Residential Properties, LLC
4328-30 Glenwick Drive
Lot 5 Block 15 of Highland Park HS Add. Dallas, TX




IKEMIRE ARCHITECTS, LLC
ARCHITECTURE PLANNING INTERIORS
16660 DALLAS PKWY. SUITE 2900 DALLAS, TX 972-248-2486 FAX 972-248-1557

SECOND FLOOR ELECTRICAL PLAN

SCALE: 1/4" = 1'-0"

E2

12 of 13
JOB #224045

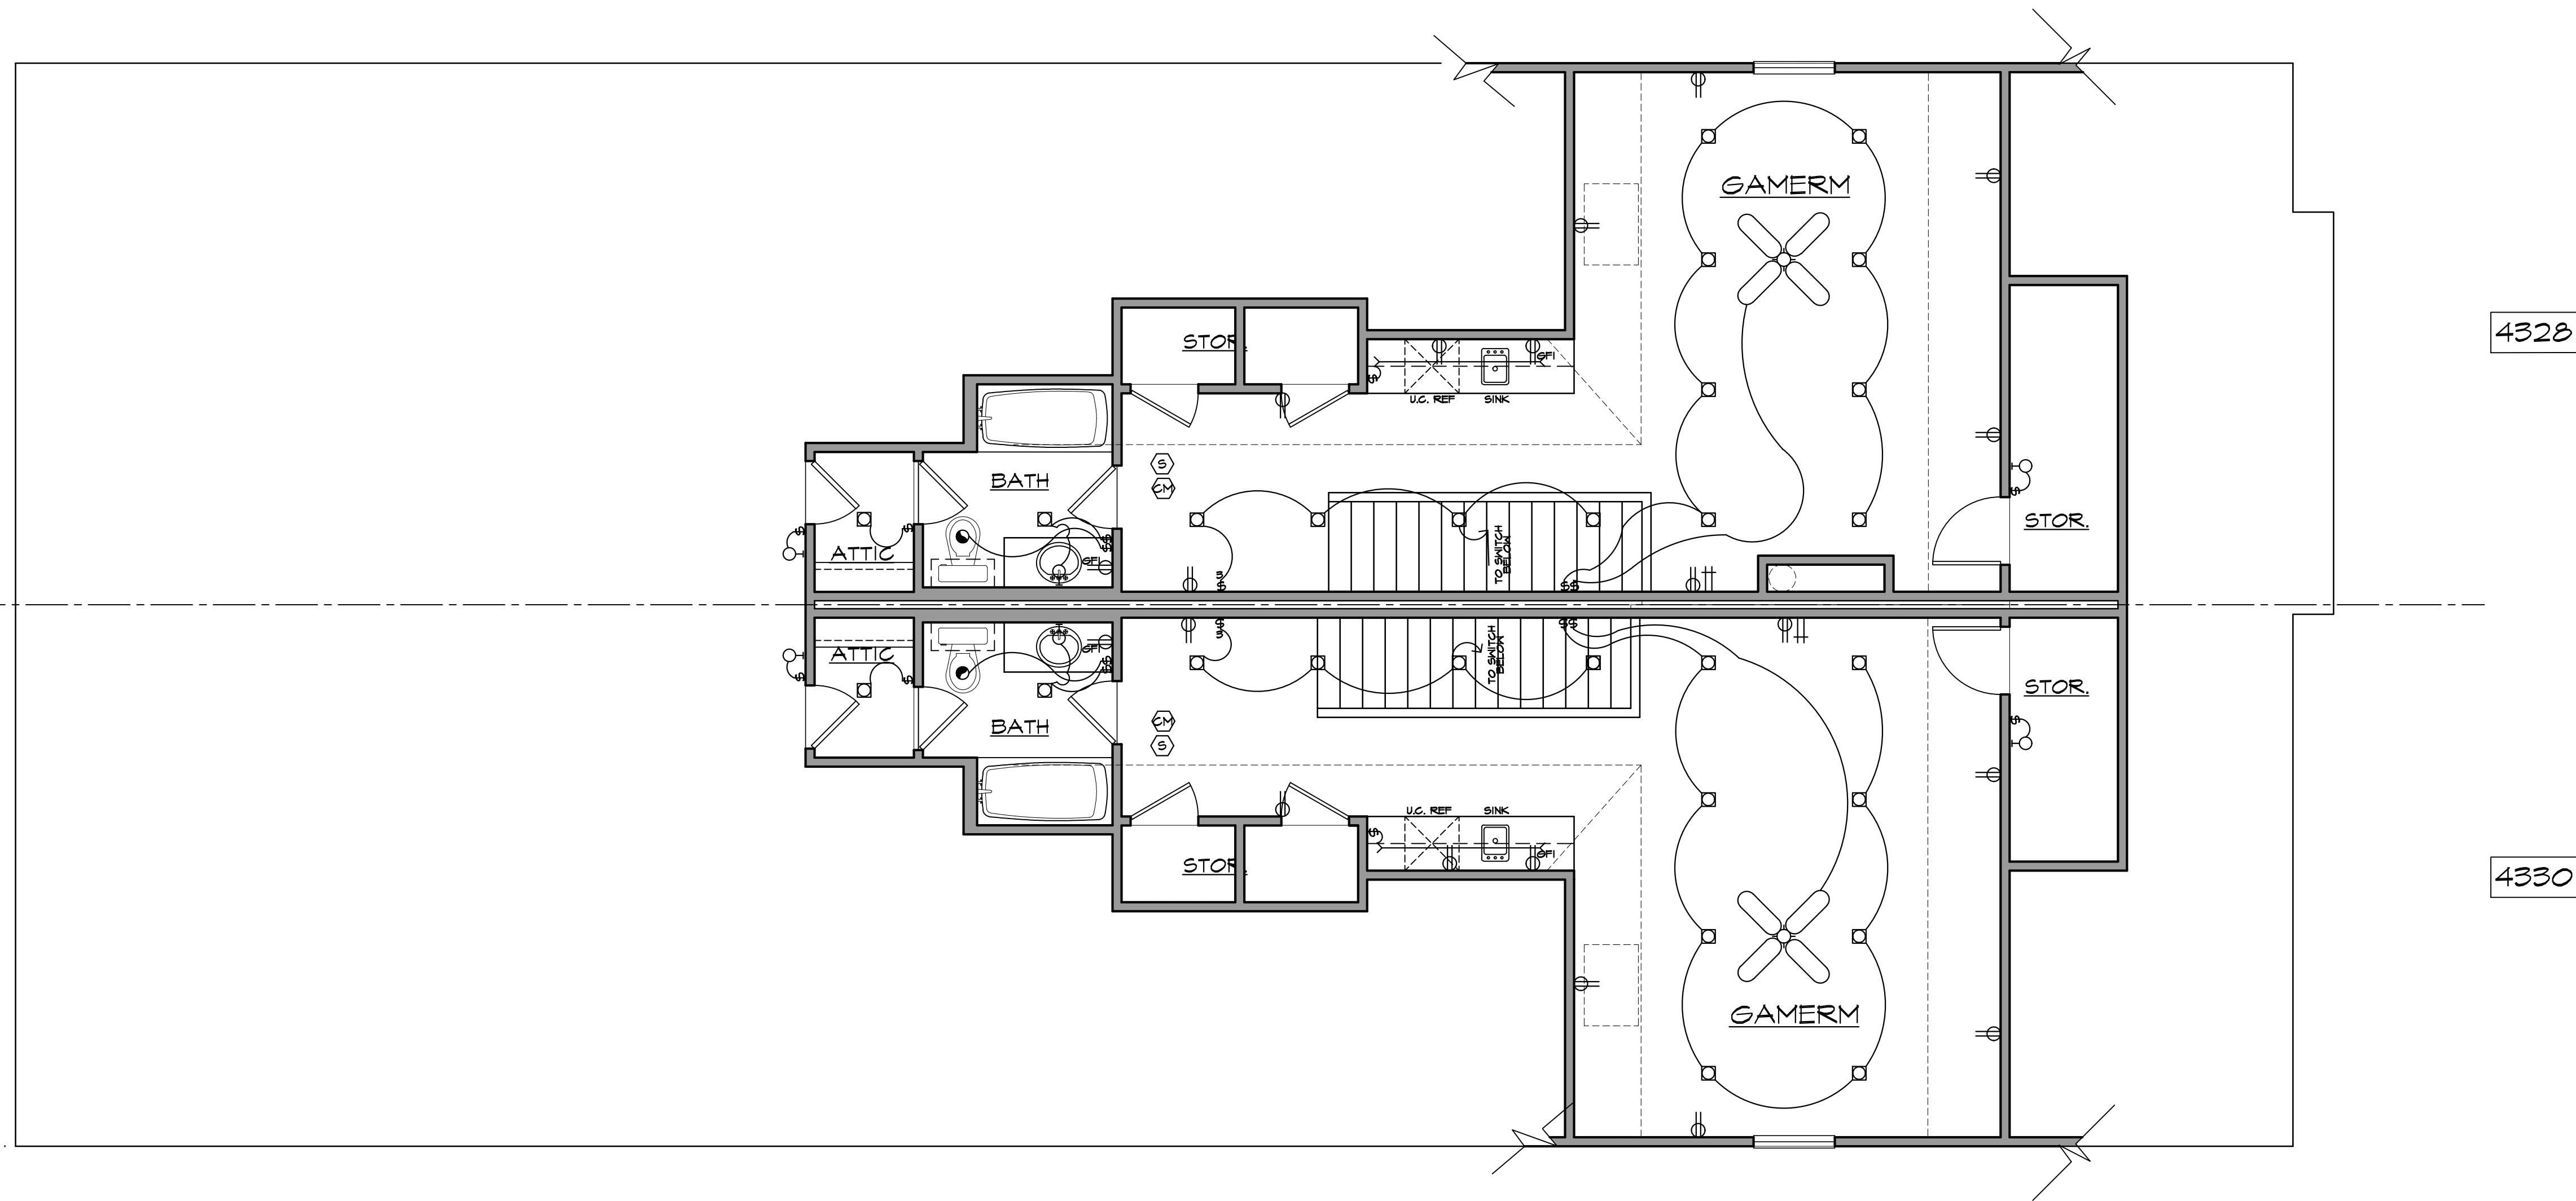

THIRD FLOOR ELECTRICAL PLAN

SCALE: 1/4" = 1'-0"

ELECTRICAL SYMBOLS			
	110V. DUPLEX		FLOOD LIGHT
	110V. DUPLEX SWITCH AT TOP ONLY		SMOKE DETECTOR
	220V. OUTLET		CARBON MONOXIDE DETECTOR
	WATERPROOF OUTLET		RECESS EYEBALL
	GROUND FAULT		CEILING MOUNTED FIXTURE
	110V. CEILING OUTLET		WALL BRACKET
	110V. FLOOR OUTLET		RECESSED CAN FIXTURE
	SINGLE POLE SWITCH		PEND. LITE
	THREE WAY SWITCH		FLUORESCENT
	DIMMER SWITCH		DRAWN TO SCALE
	110V. JUNCTION BOX		UNDER / OVER CABINET FLUORESCENT LITE
	EXHAUST FAN		GAS OUTLET
	DOORBELL		TELEVISION OUTLET
	DOORBELL CHIME		TELEPHONE OUTLET
	CLG. FAN W/ LIGHT FIXT.		SERVICE PANEL
			GARAGE DOOR OPENER

NOTE: ADD OUTLETS AS REQUIRED BY 2020 NATIONAL ELECTRIC CODE.



IKEMIRE ARCHITECTS, LLC
ARCHITECTURE PLANNING INTERIORS
16660 DALLAS PKWY. SUITE 2900 DALLAS, TX 75248-2486 FAX 972-248-1557

Glenwick Drive SF/A
JGH, LLC/JG Residential Properties, LLC
4328-30 Glenwick Drive
Lot 5 Block 15 of Highland Park HS Add. Dallas, TX